




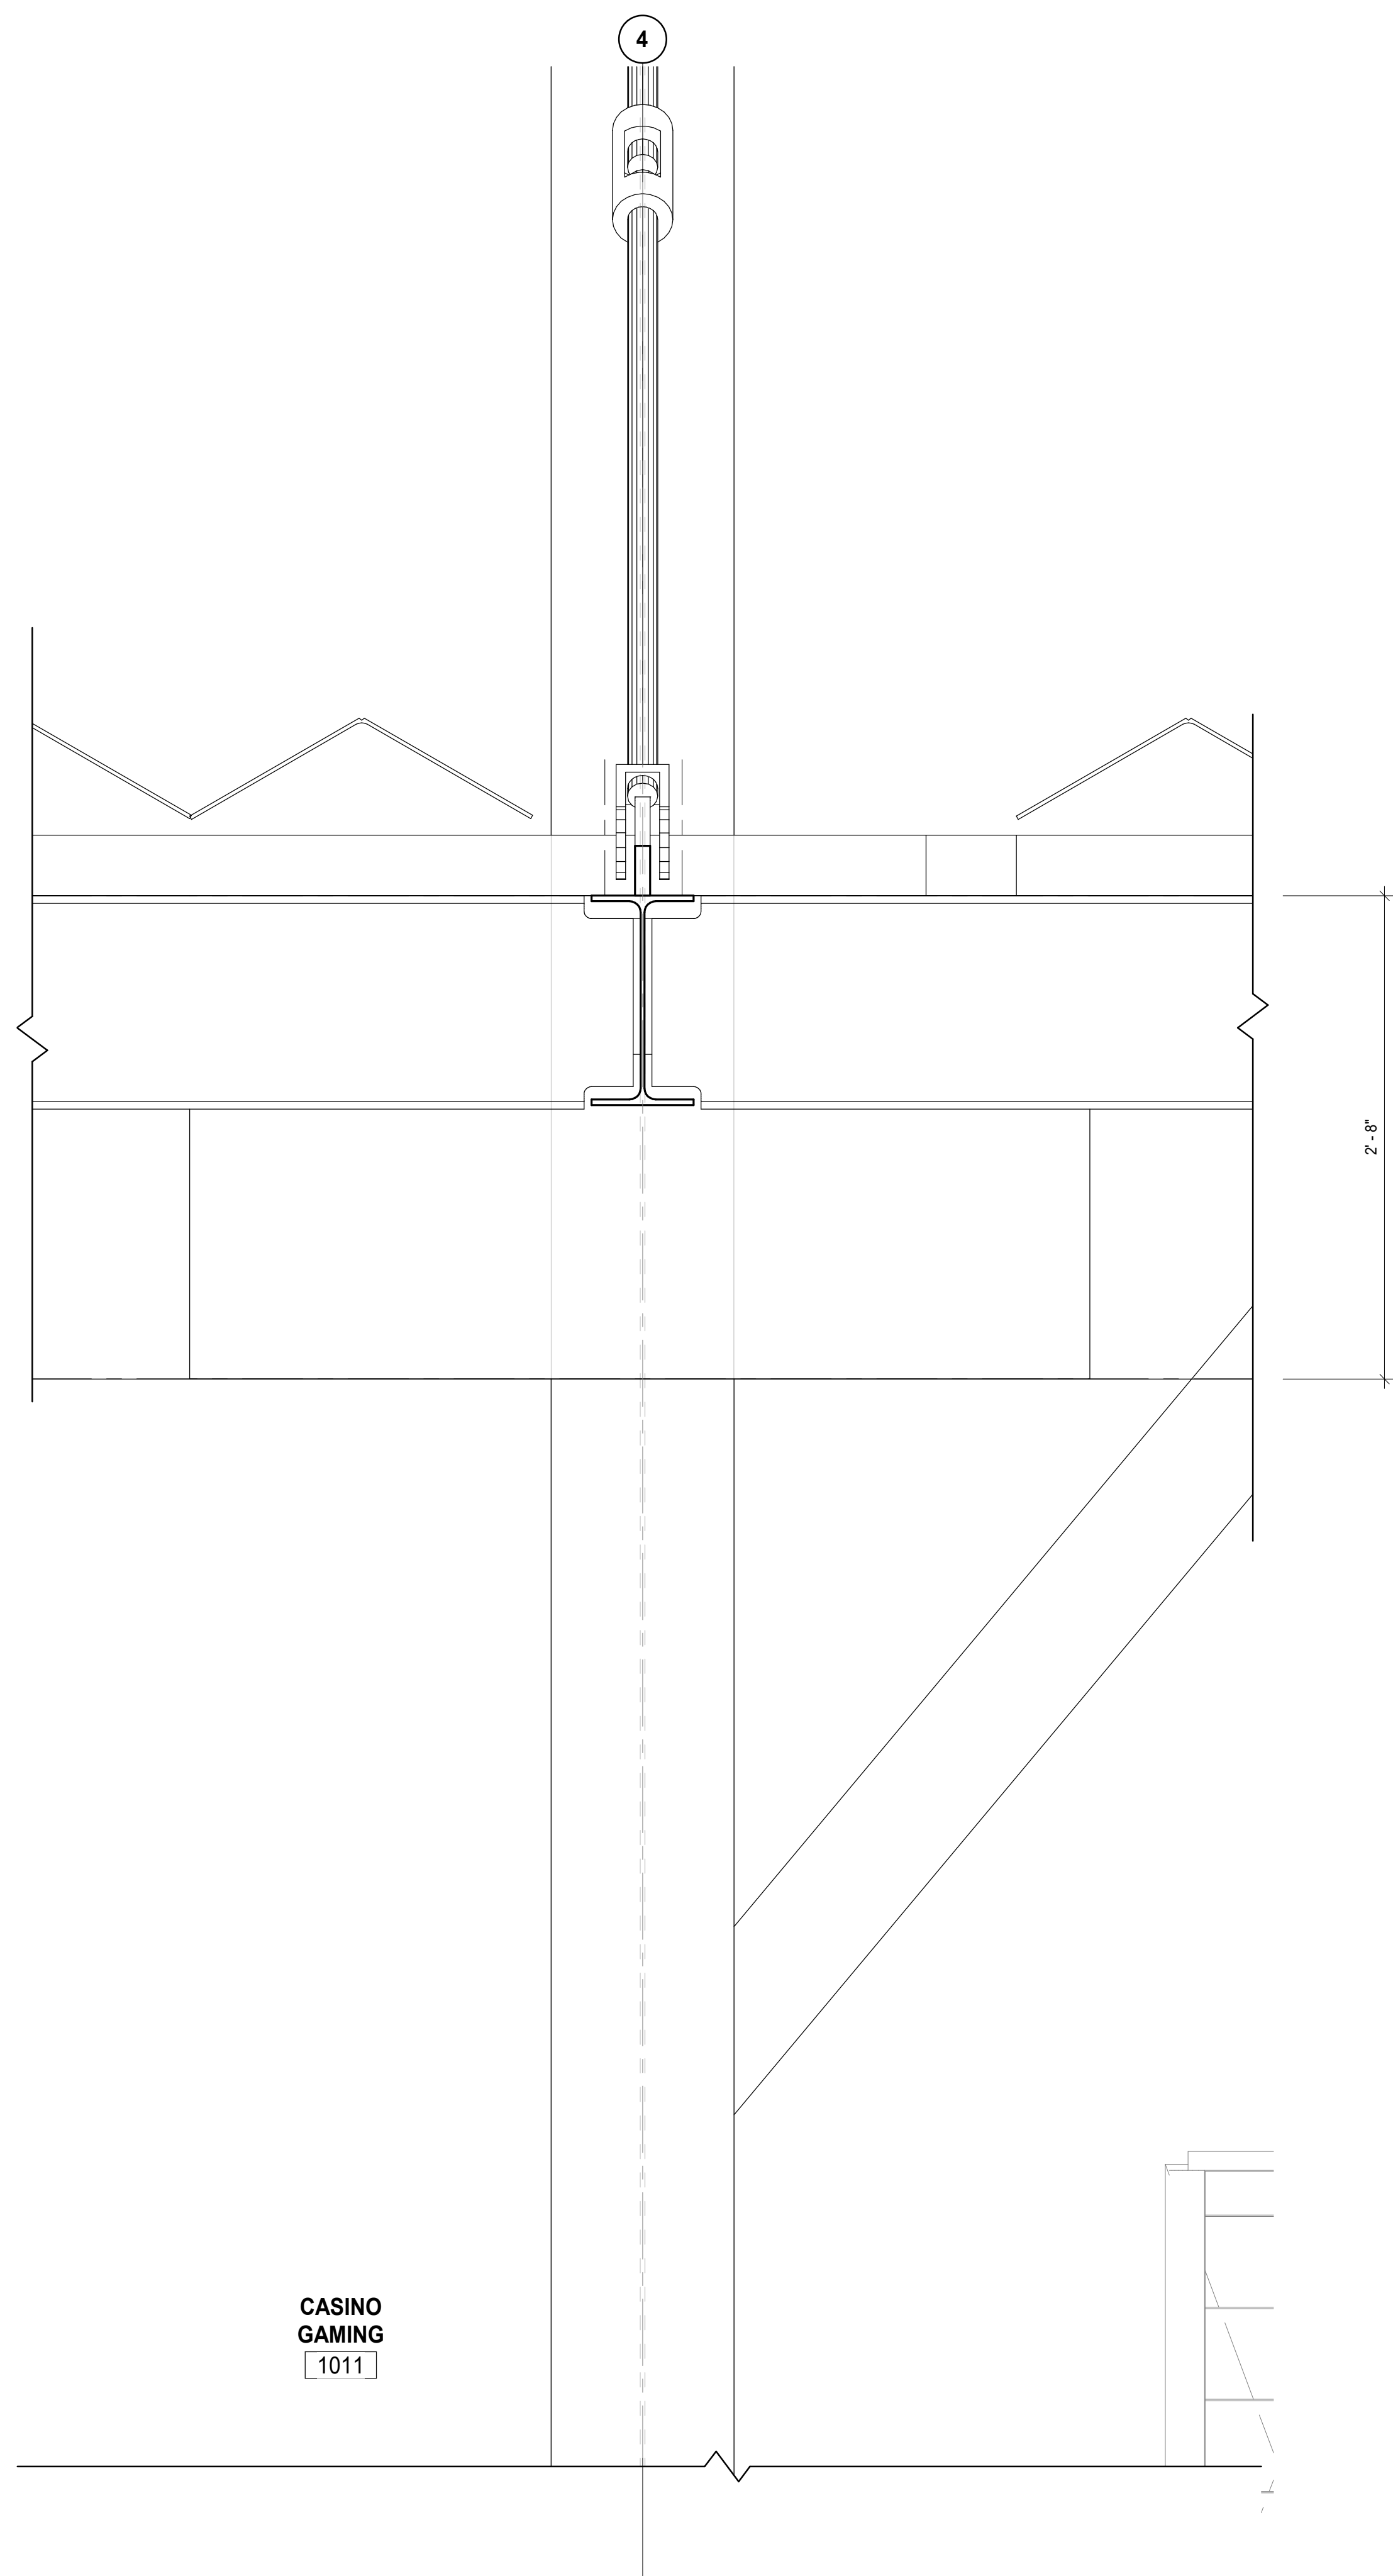


7 SECTION DETAIL AT EQUIPMENT PLATFORM
SCALE: 1 1/2" = 1'-0"

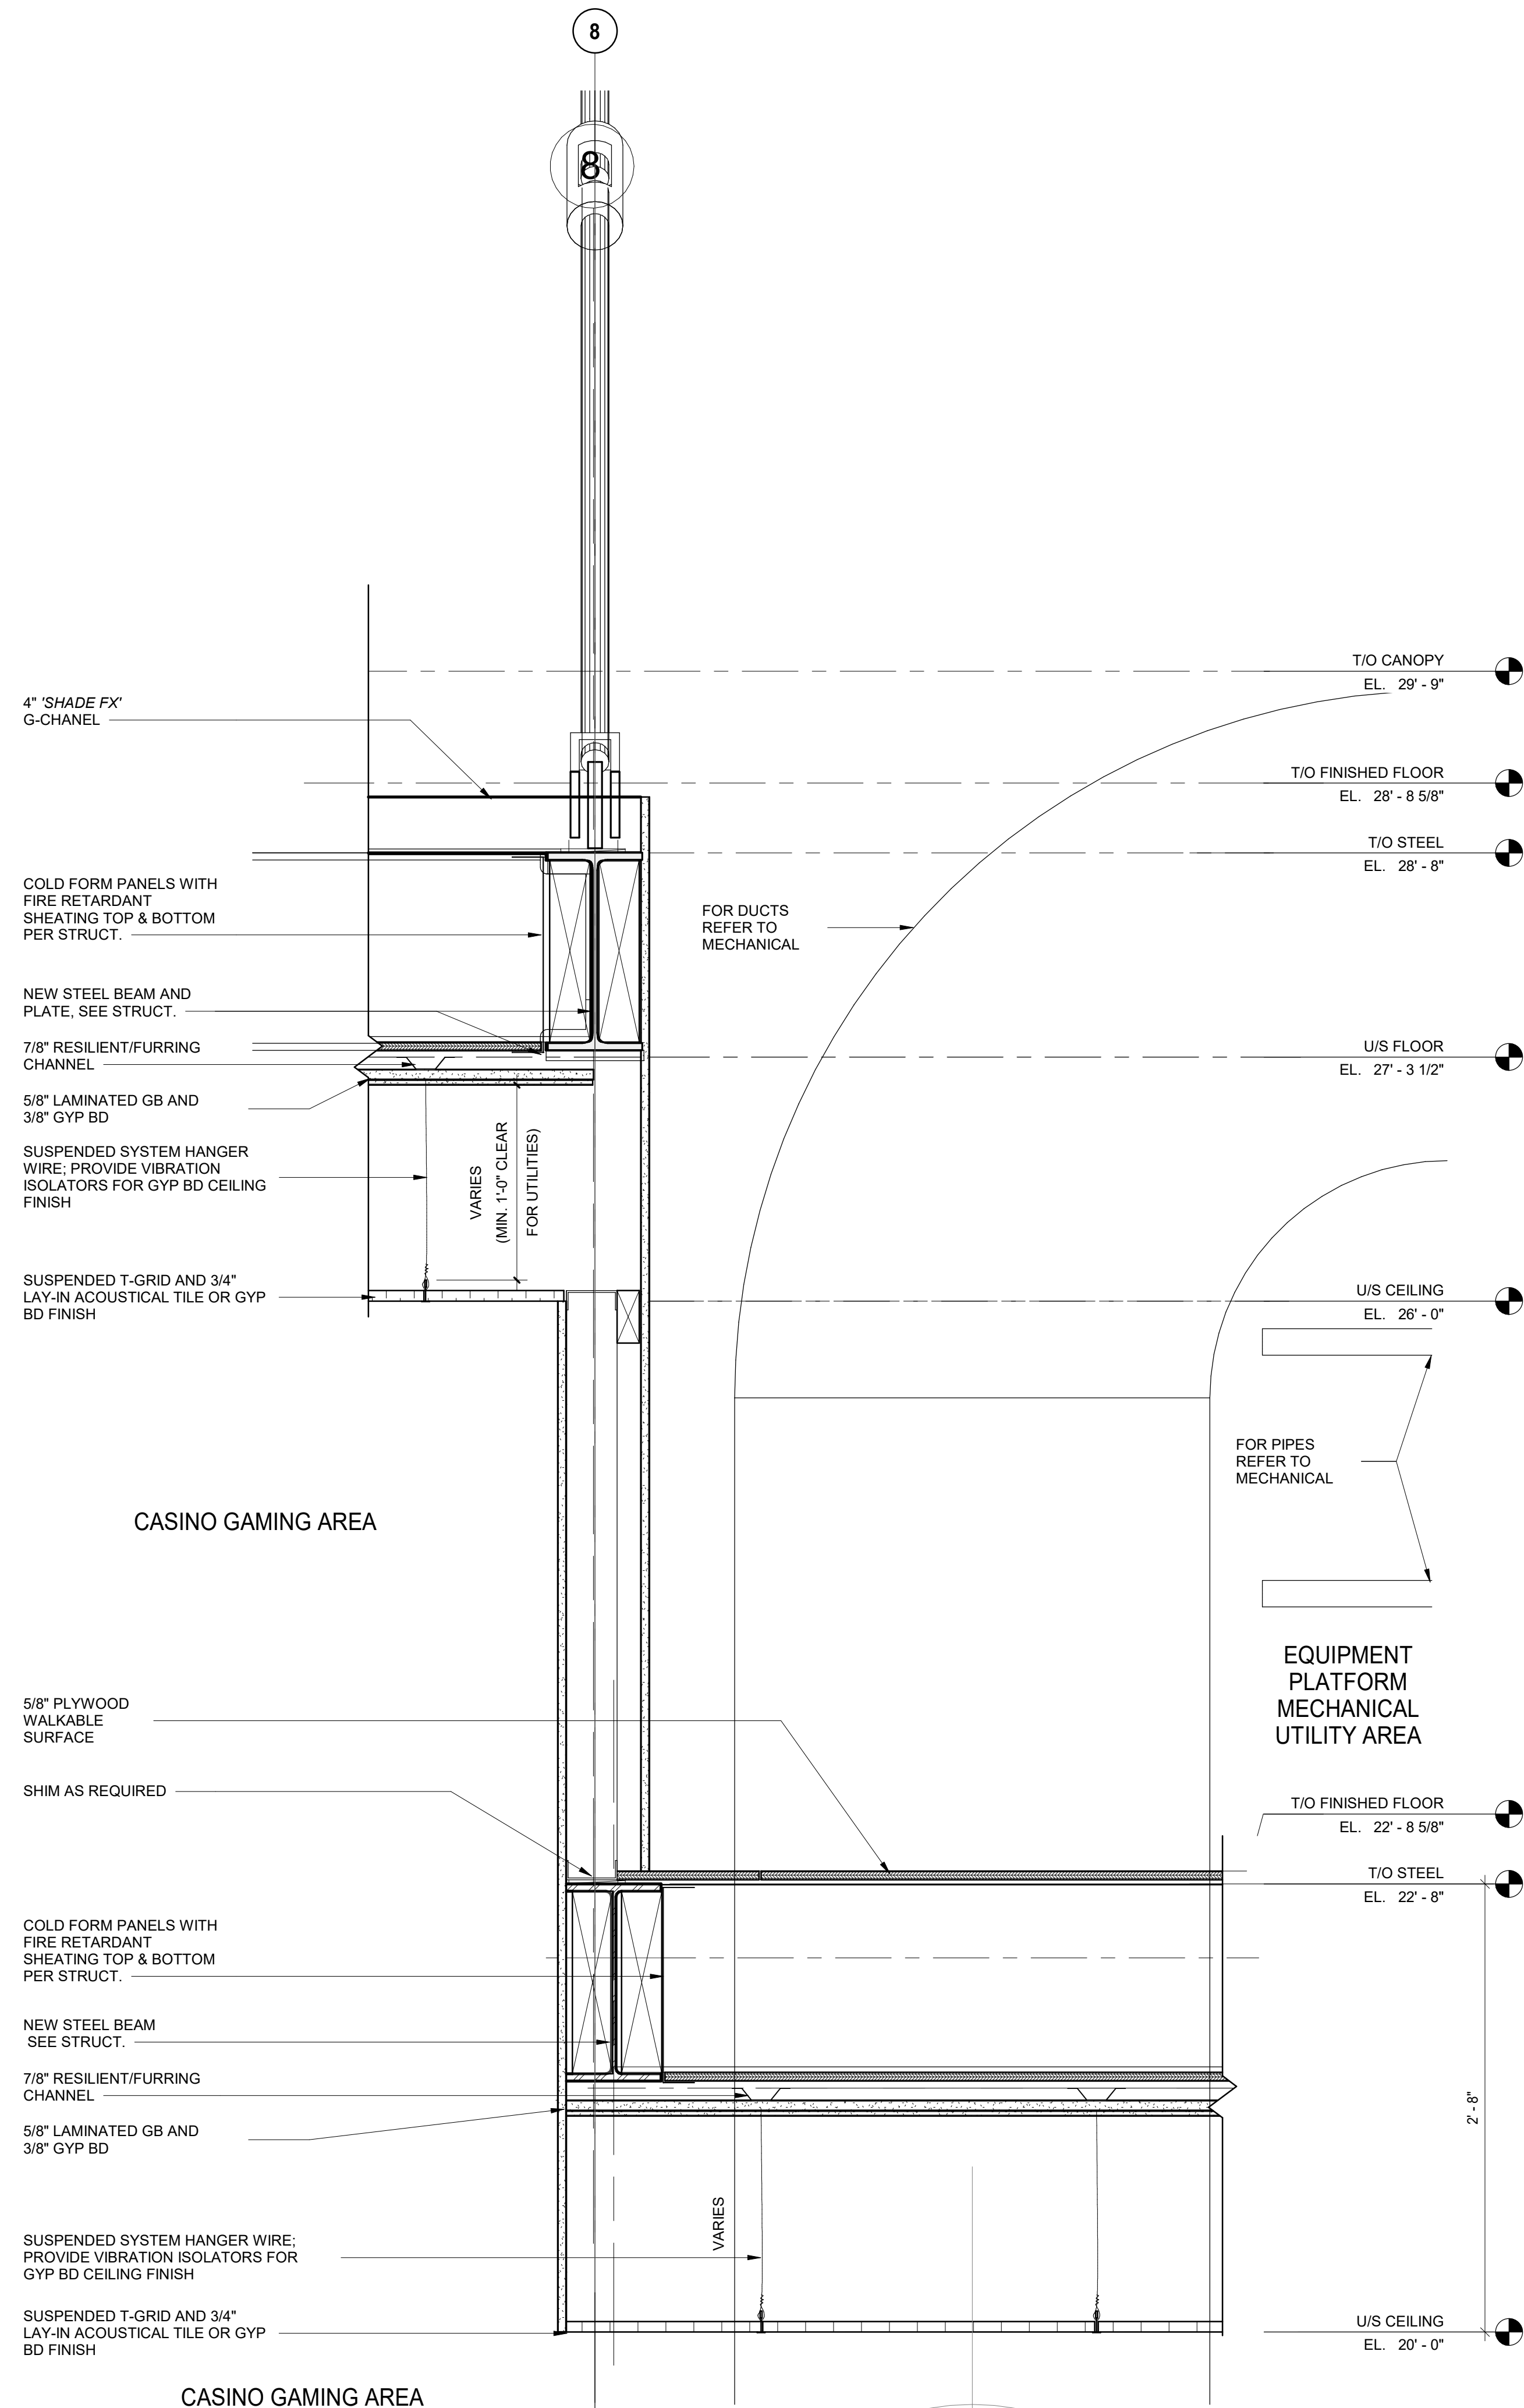


6 CEILING DETAIL AT PLATFORM TRANSITION
SCALE: 1 1/2" = 1'-0"

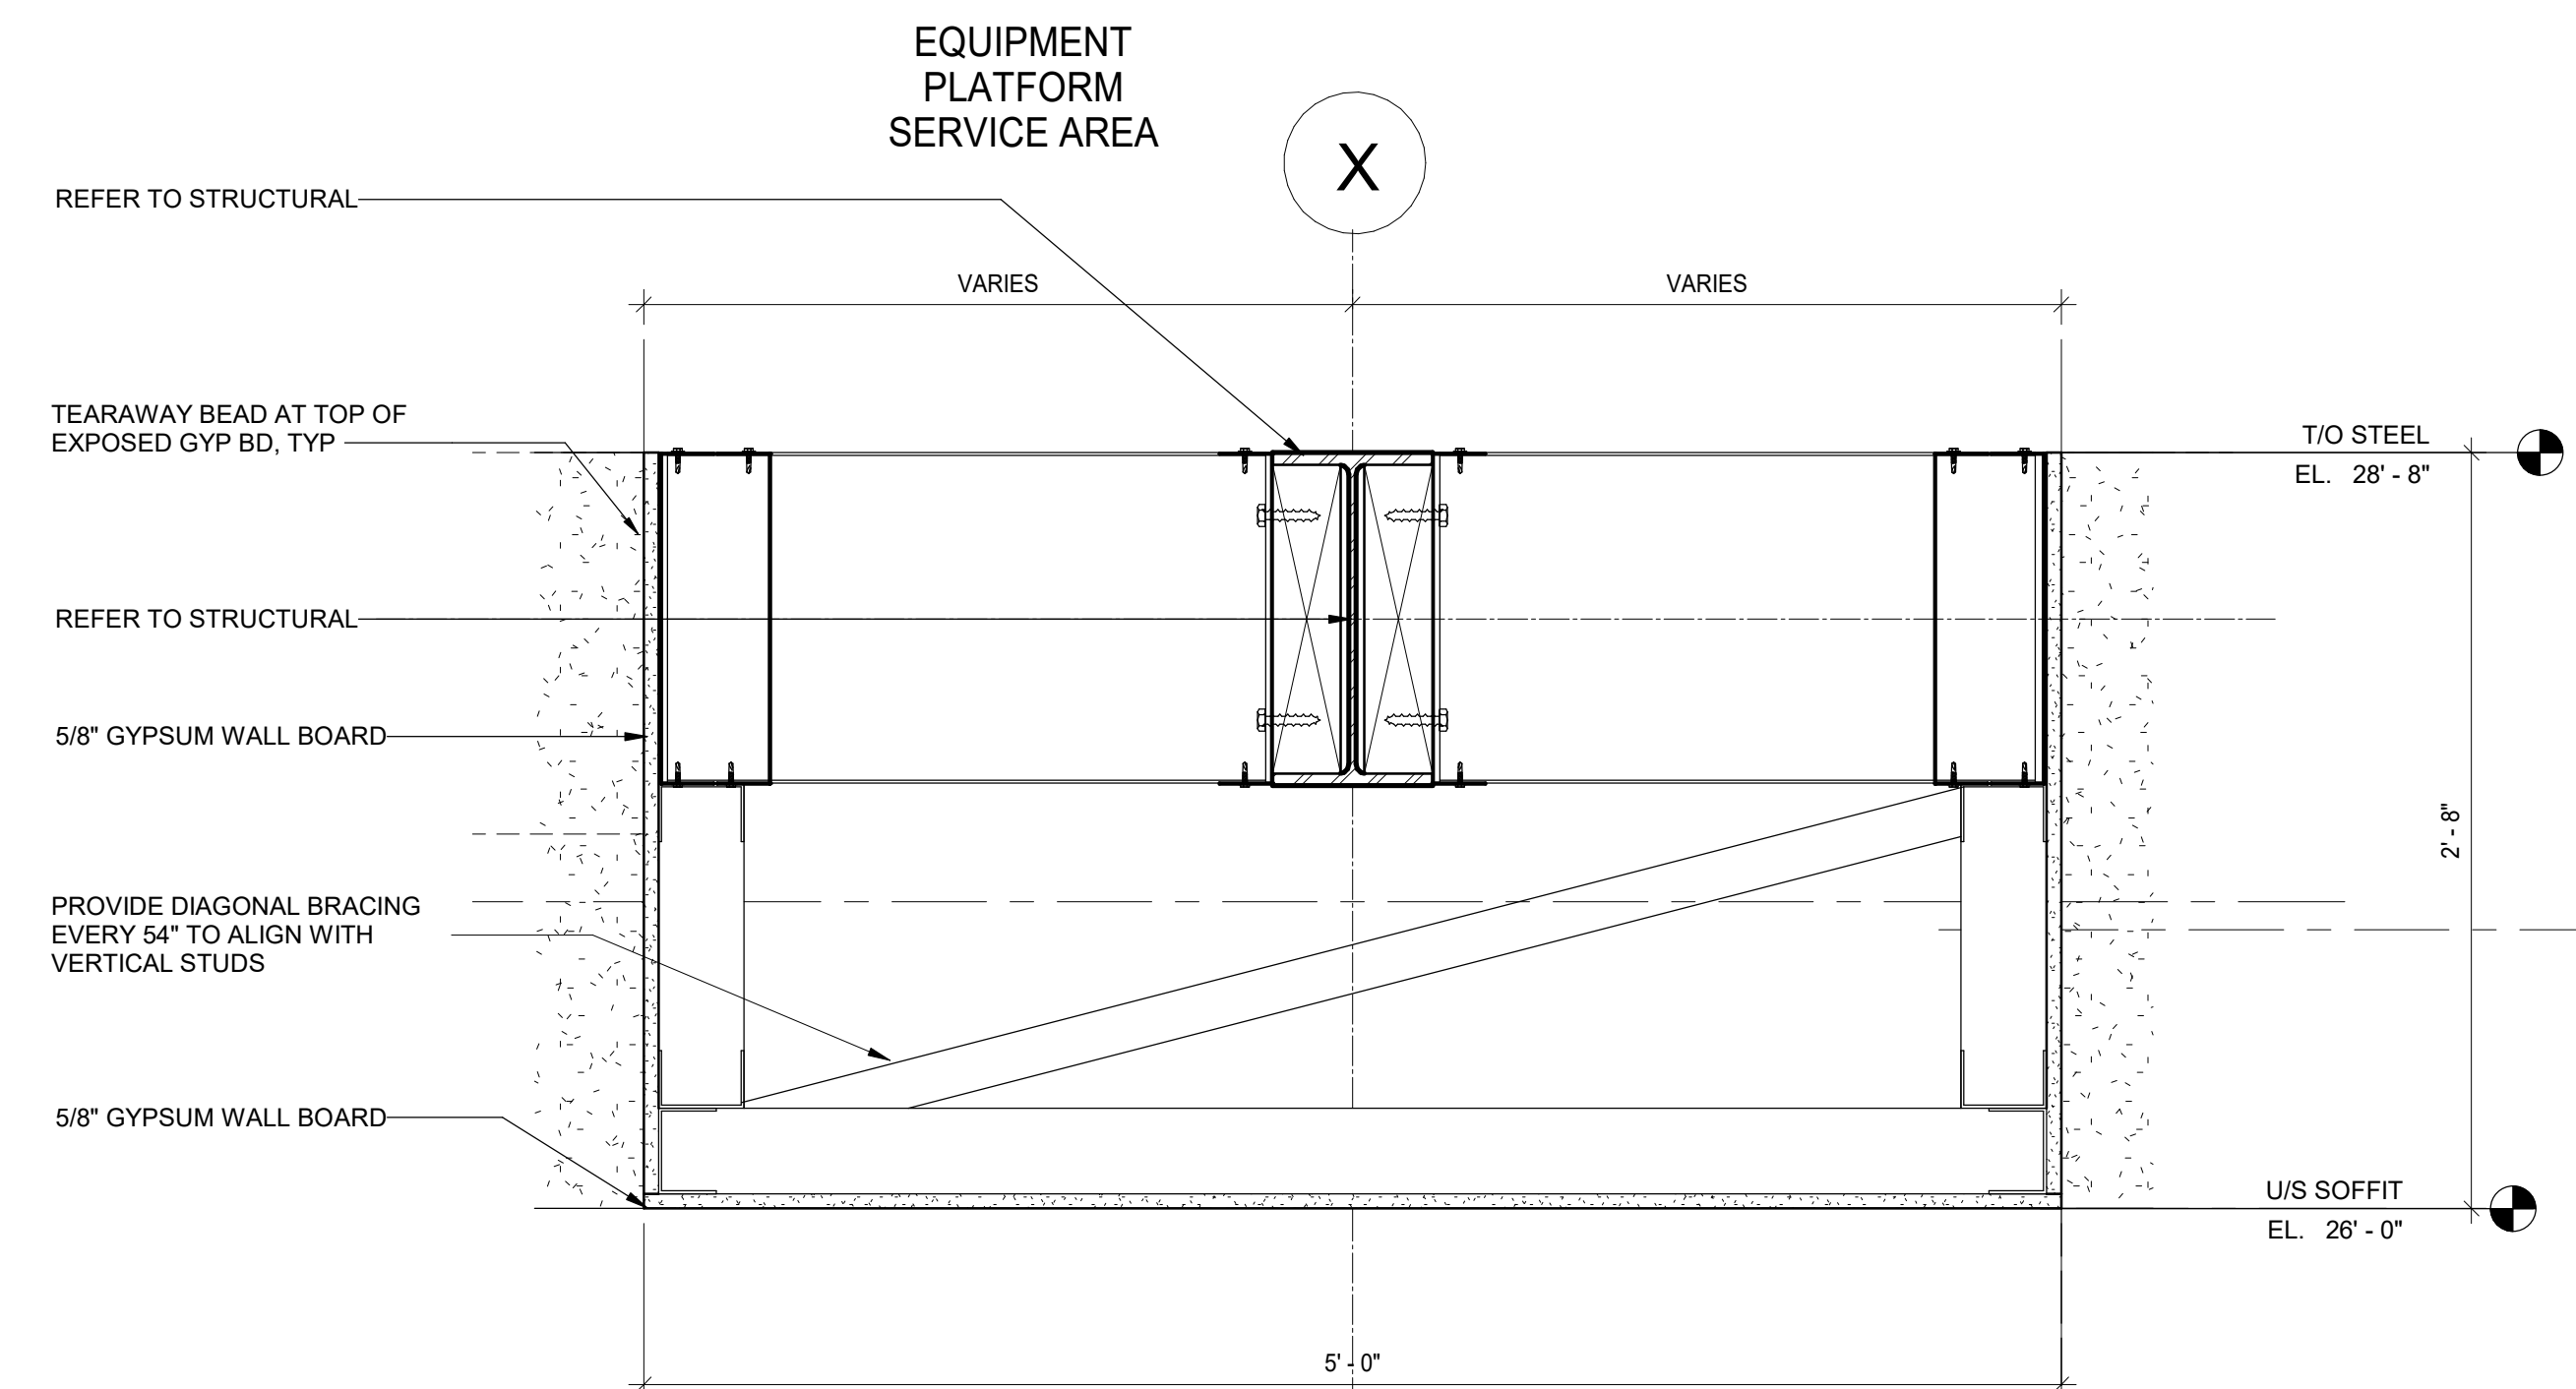


5 CEILING DETAIL AT SOFFIT (TYPICAL)
SCALE: 1 1/2" = 1'-0"

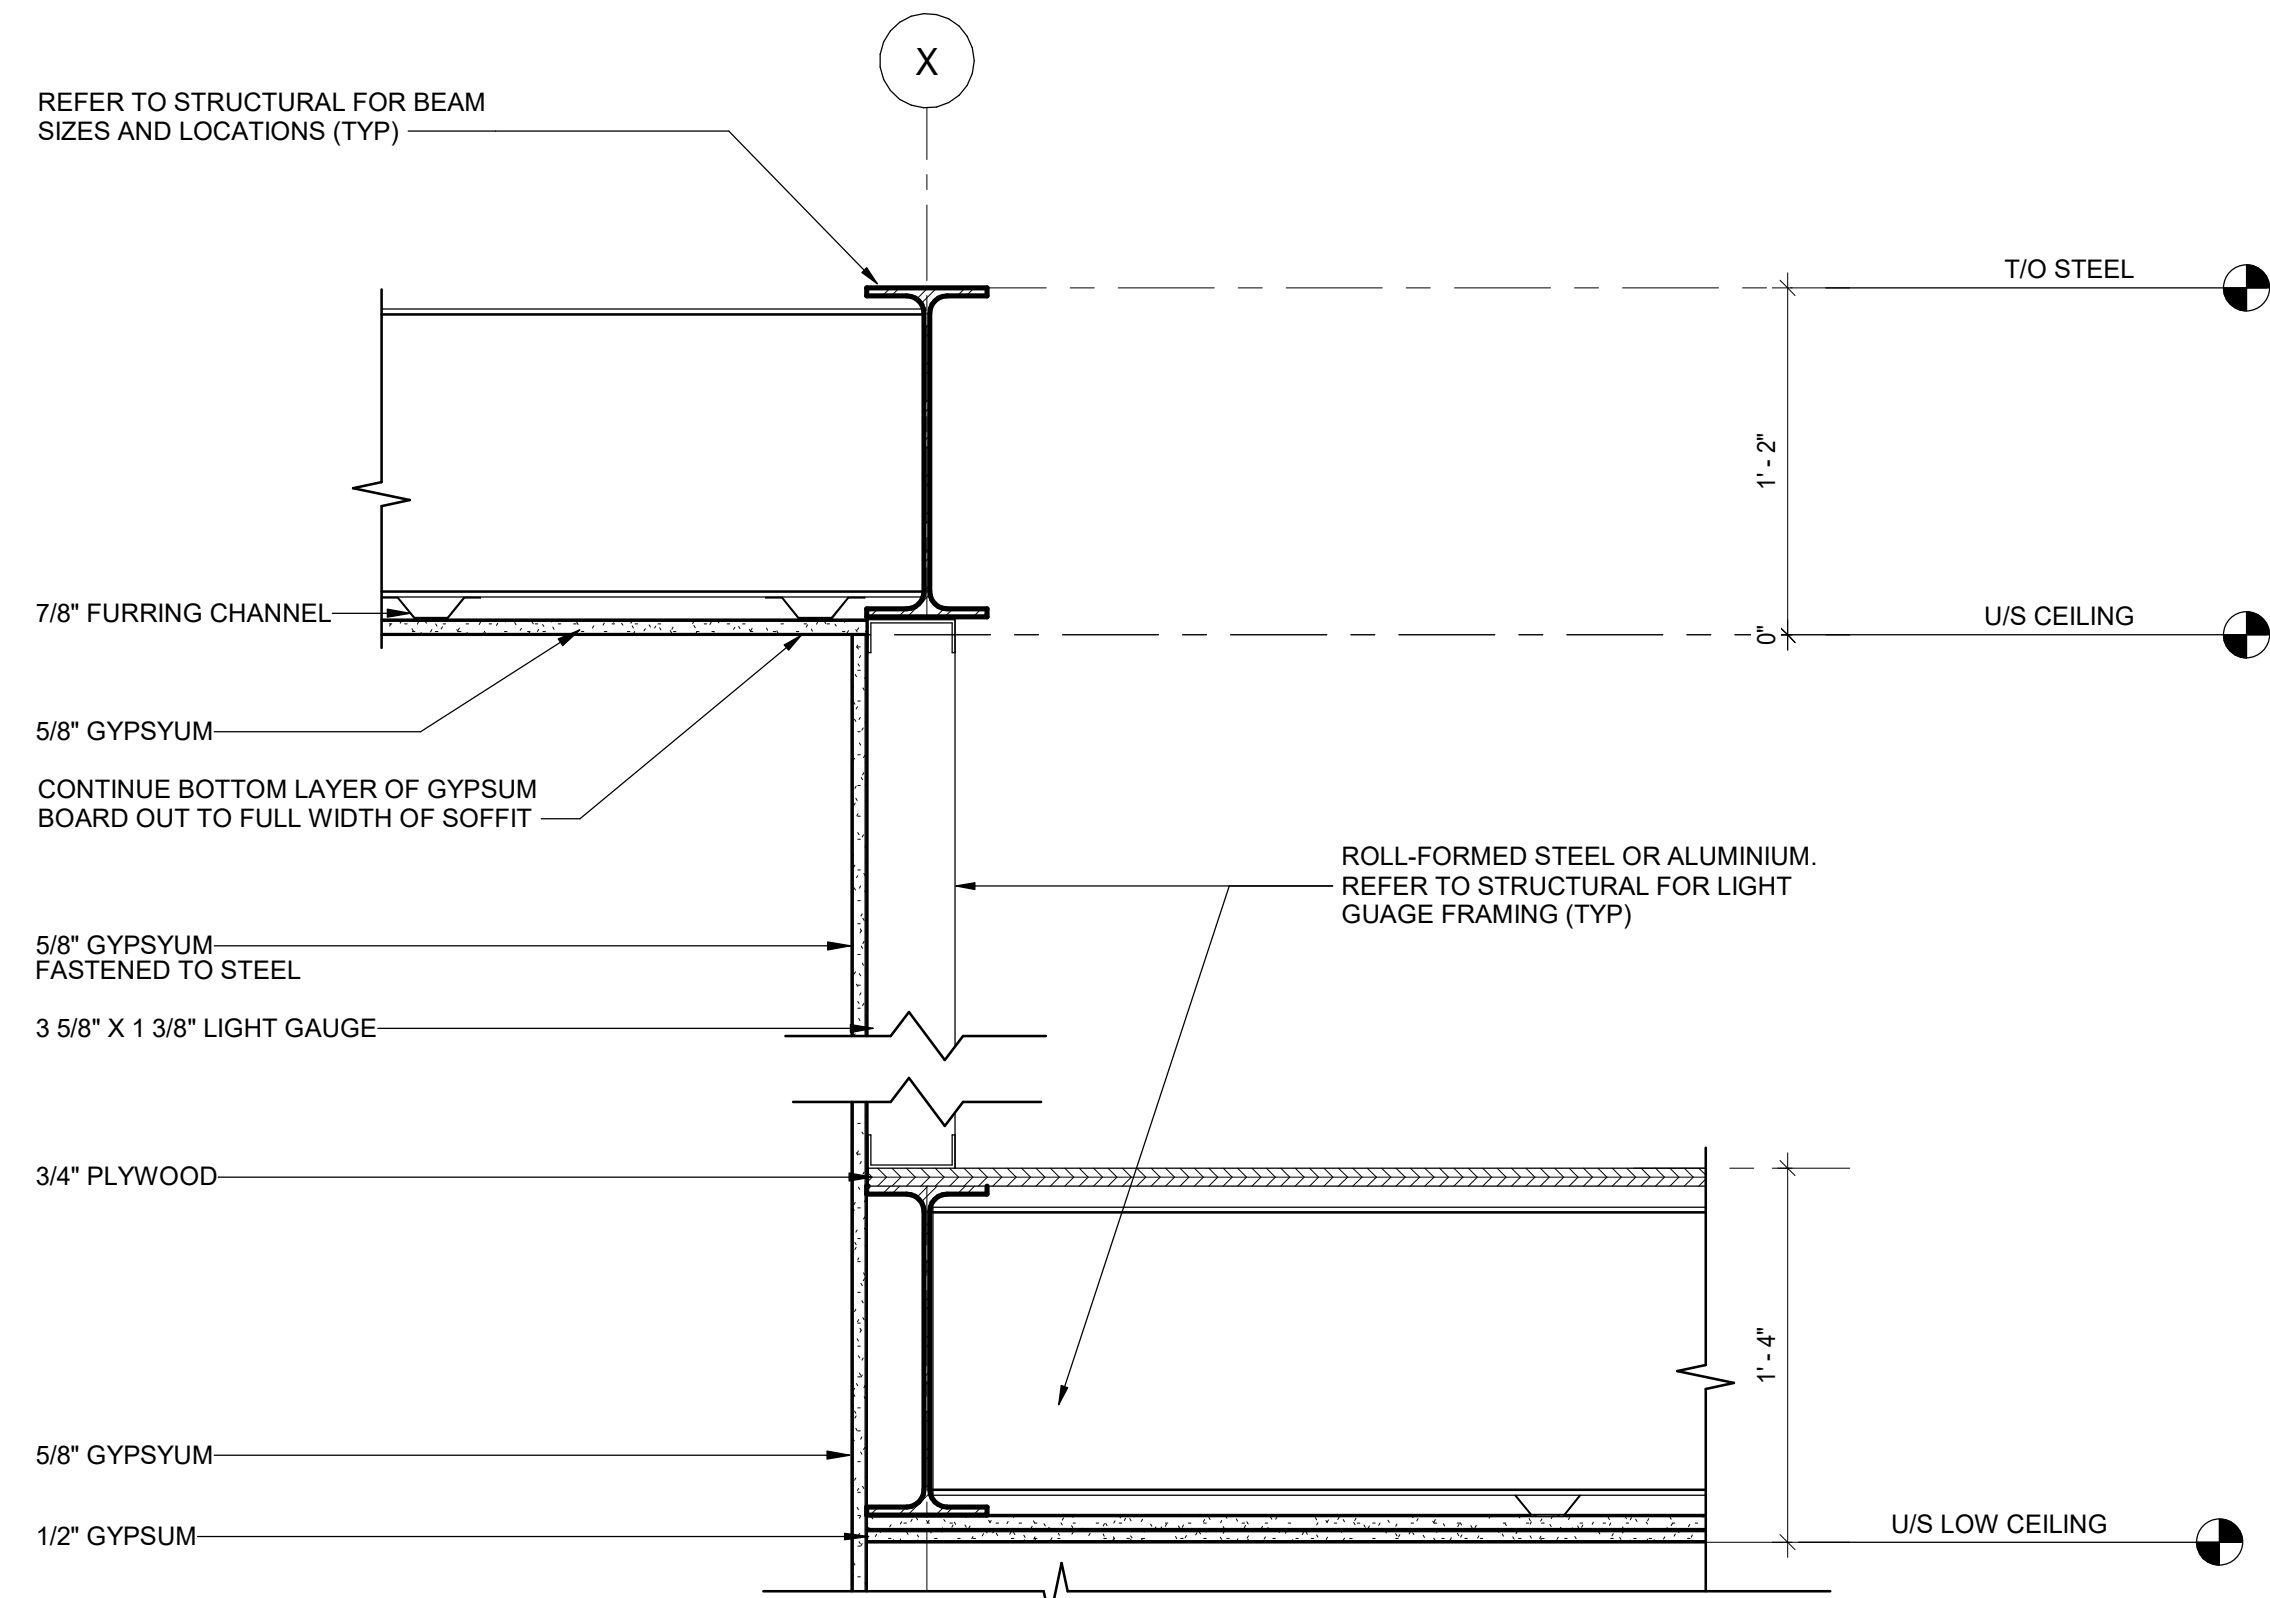

4 CEILING DETAIL - METAL LINEAR CEILING SYSTEM CARRIER AT RECEPTION - 'KNEE-WALL' (TYPICAL)
SCALE: 1 1/2" = 1'-0"

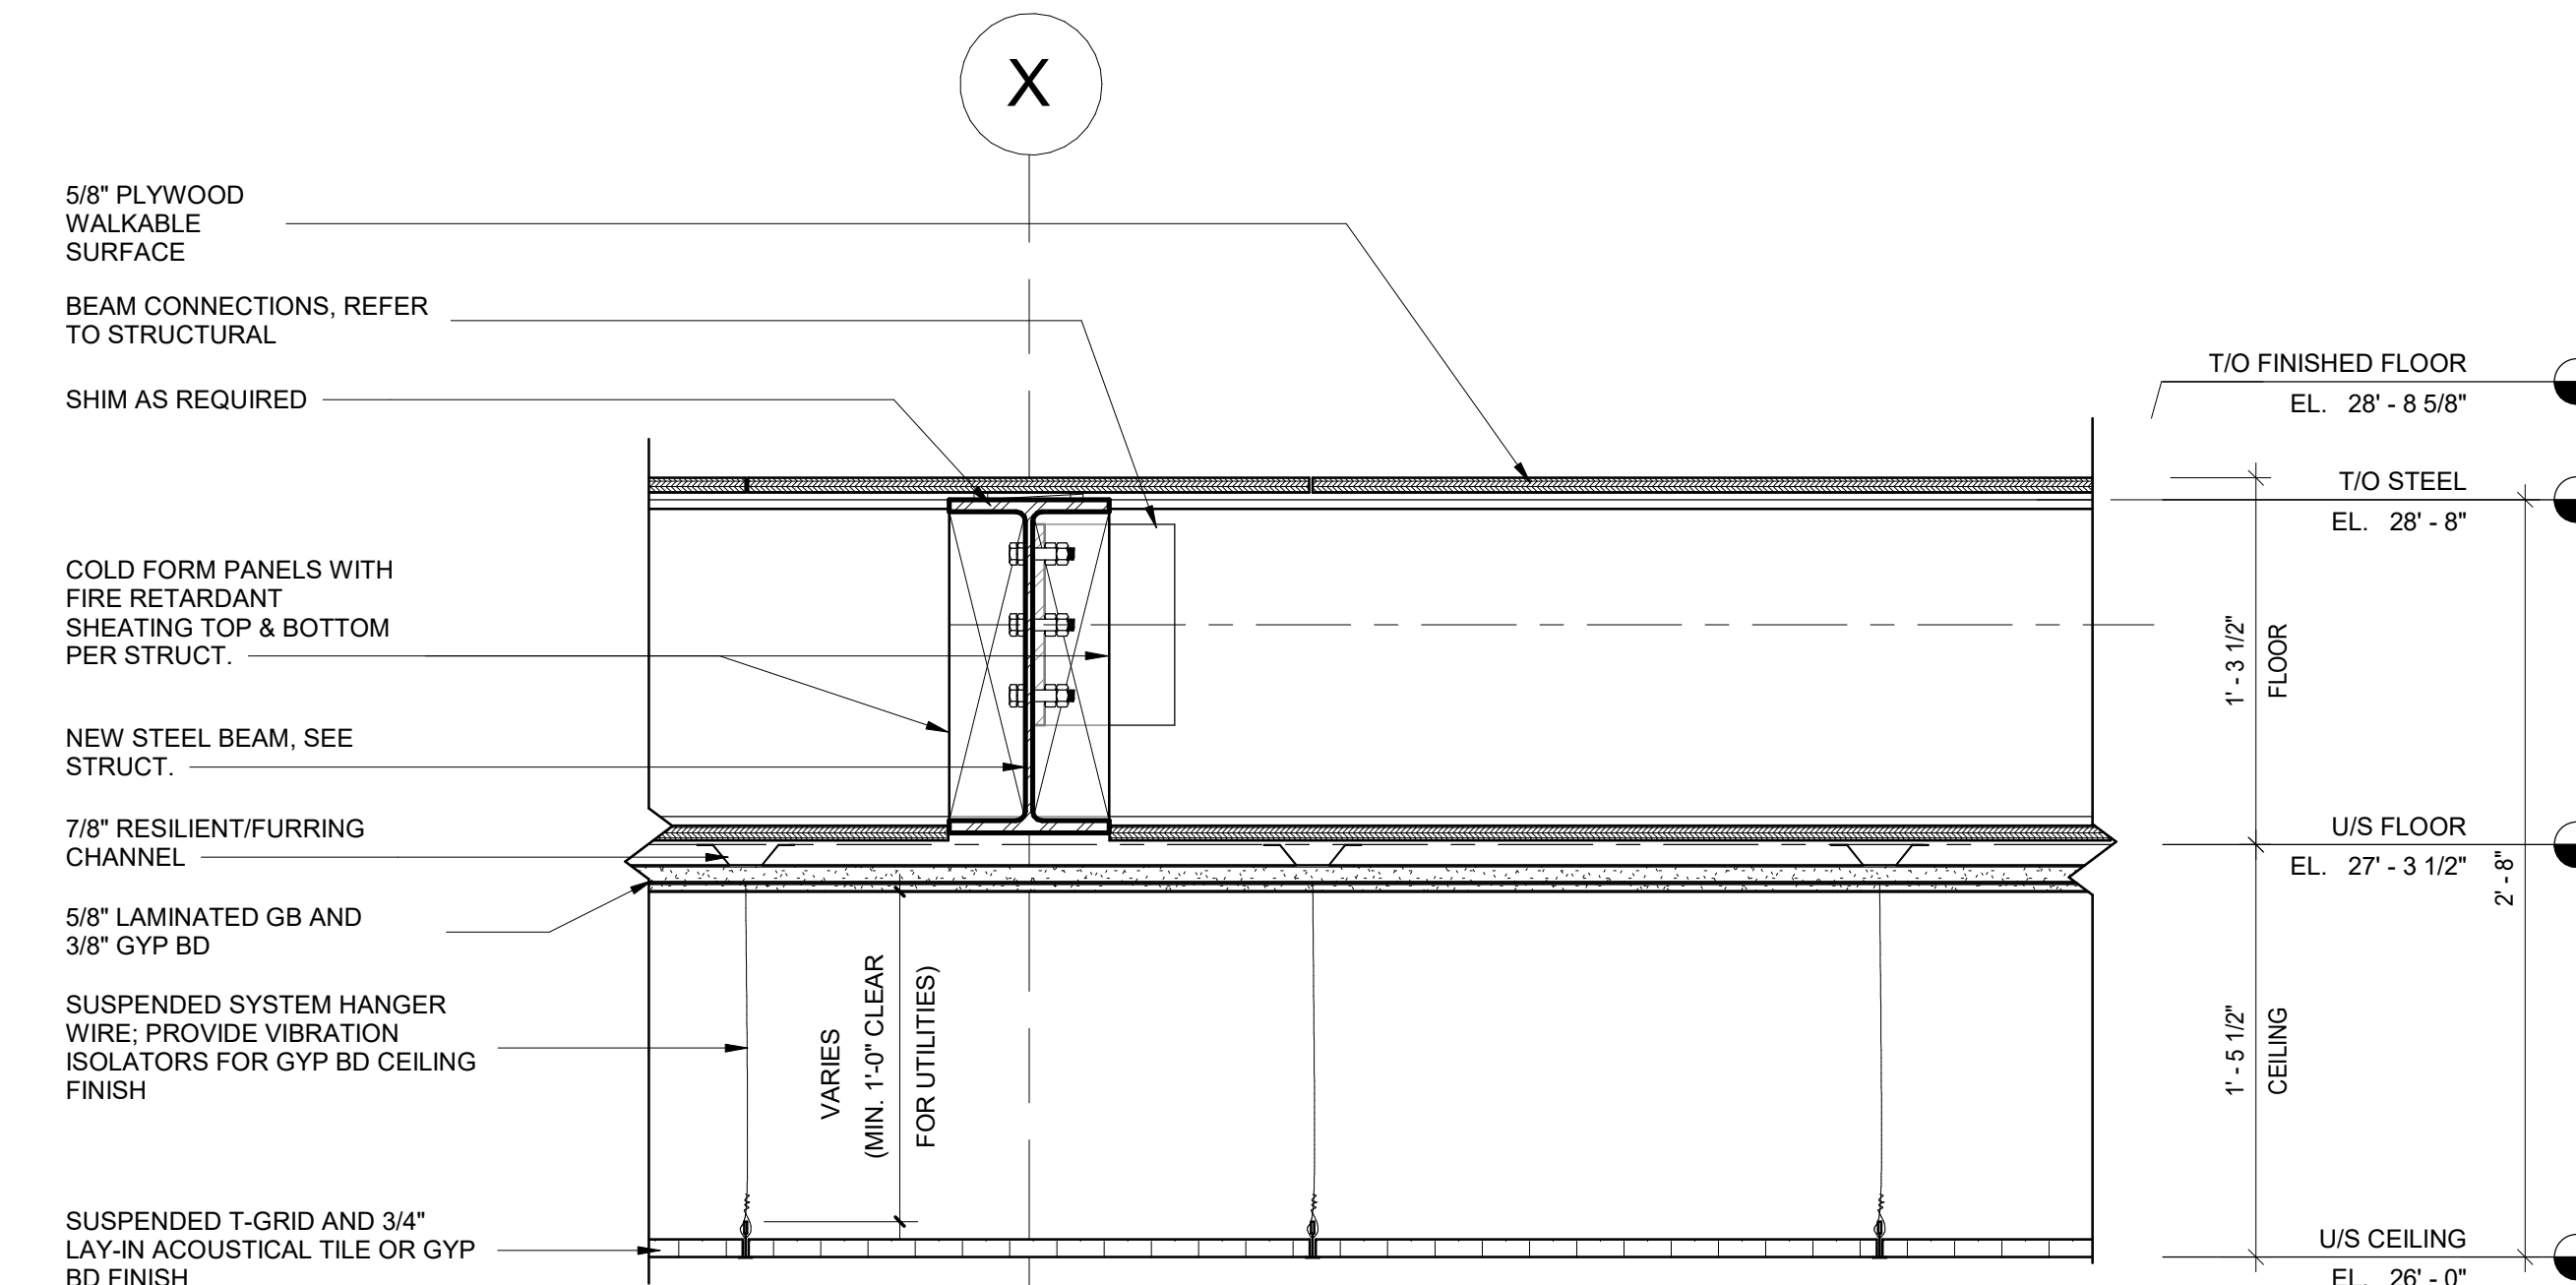

2 CEILING DETAIL - CASINO CEILING ASSEMBLY - NON-WALKABLE
SCALE: 1 1/2" = 1'-0"

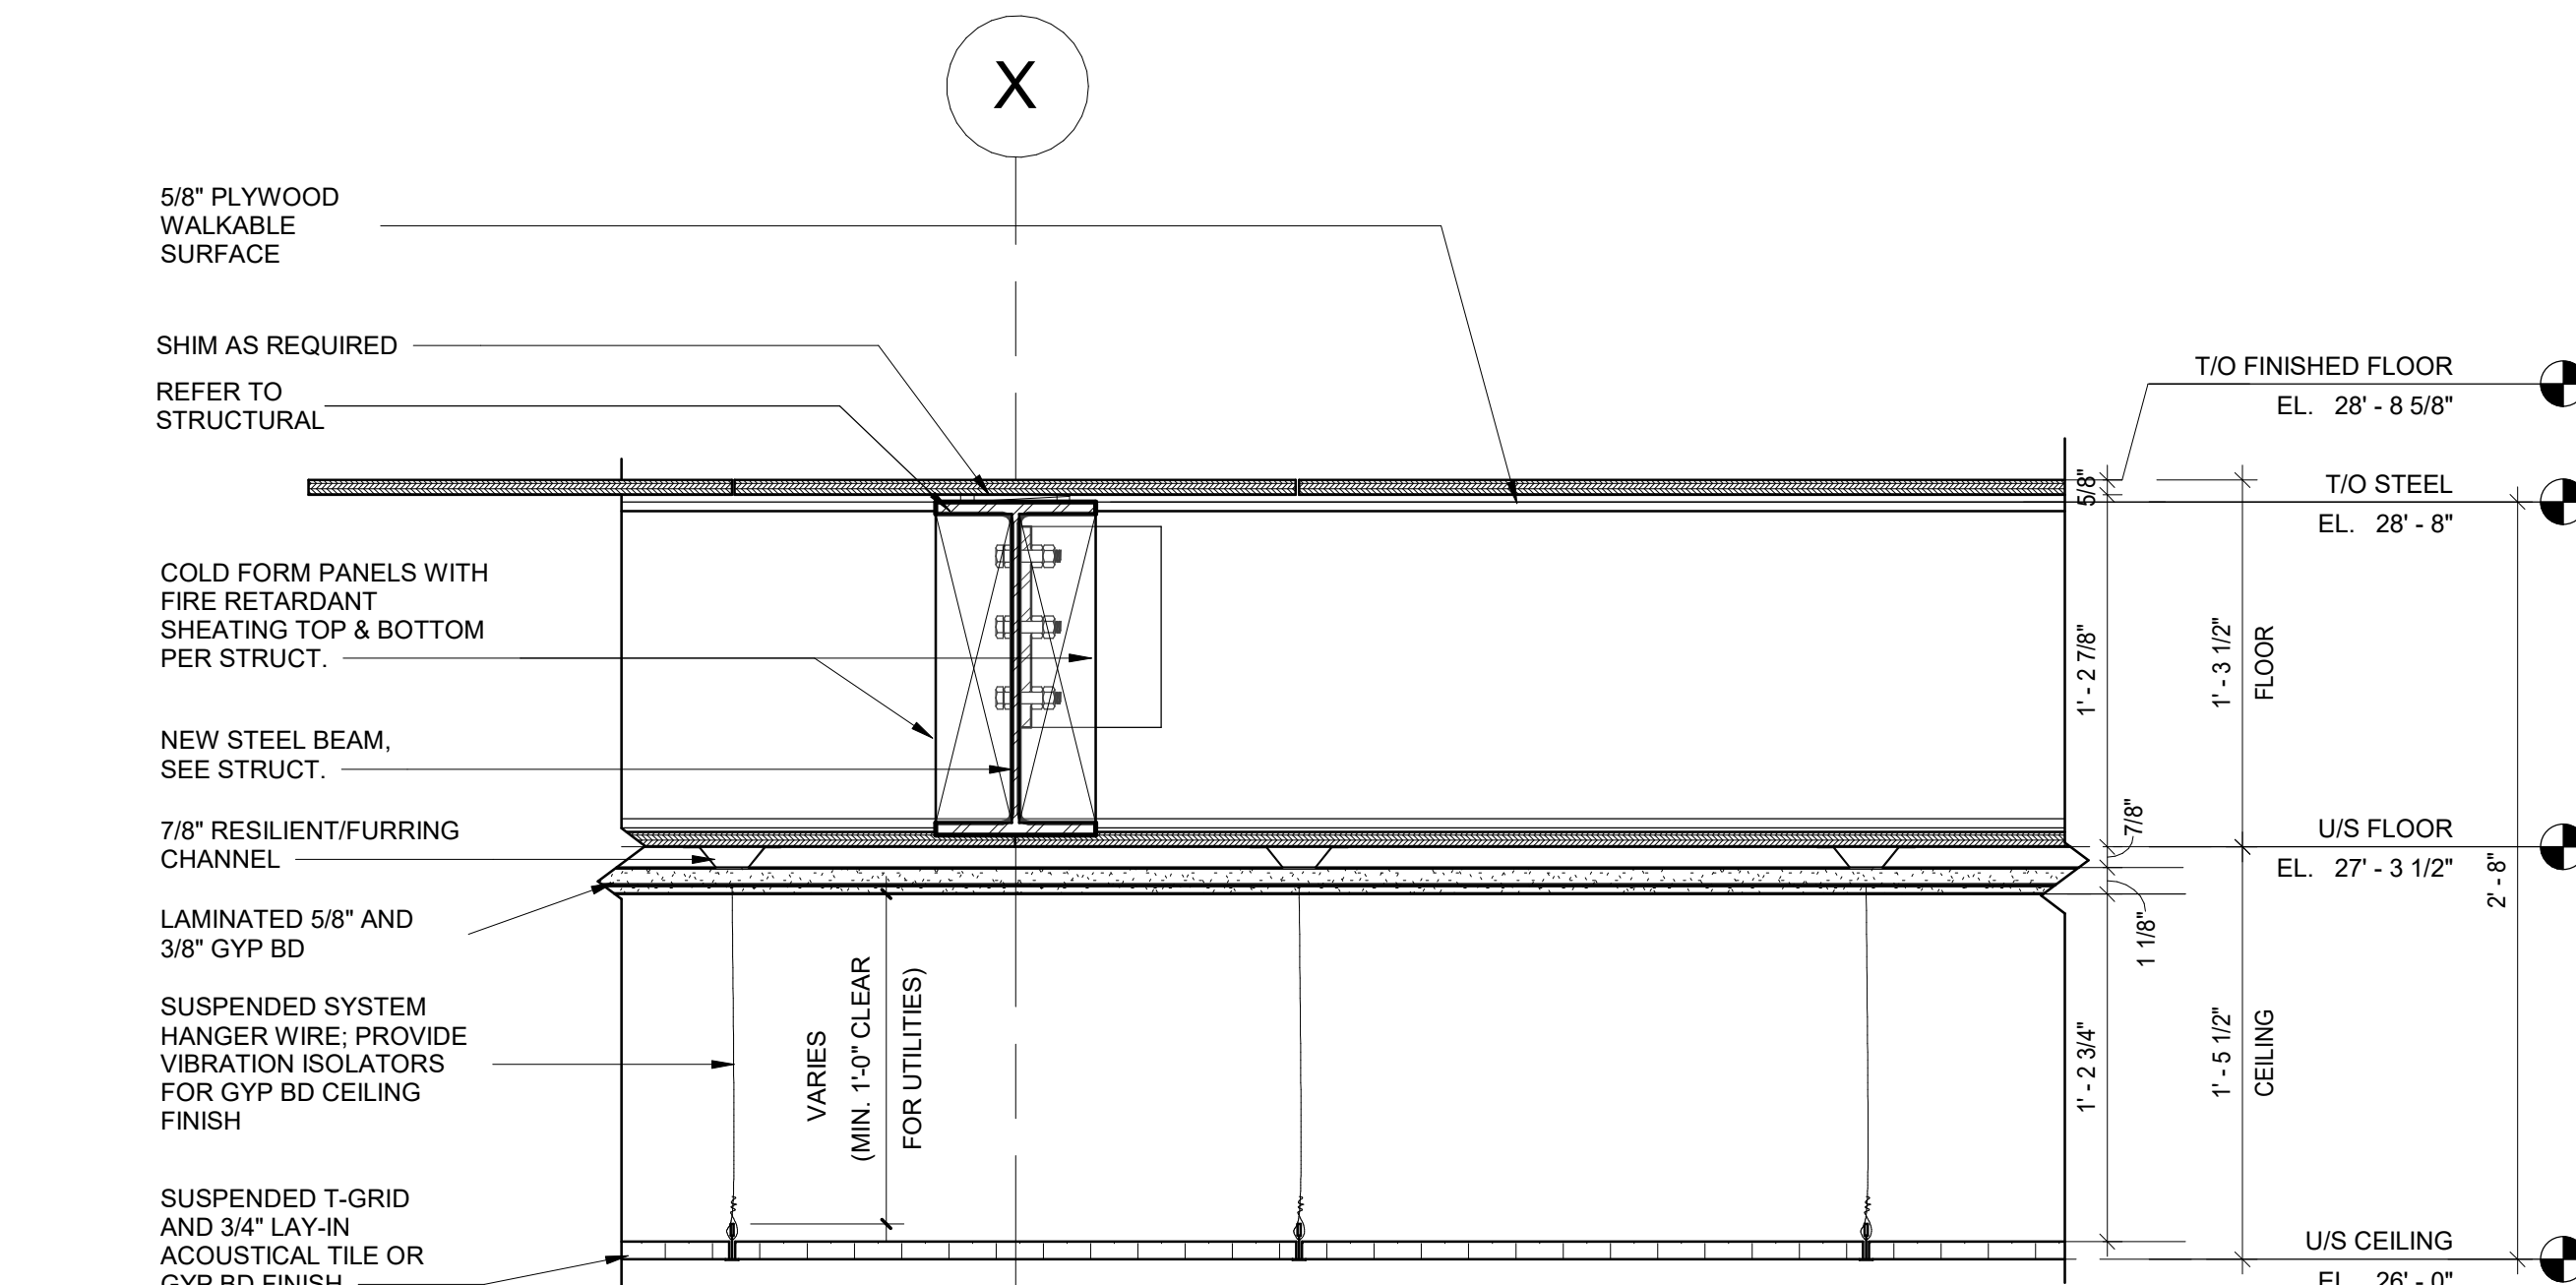

1 CEILING DETAIL - CASINO CEILING ASSEMBLY - WITH WALKABLE EQUIPMENT PLATFORM ABOVE
SCALE: 1 1/2" = 1'-0"