


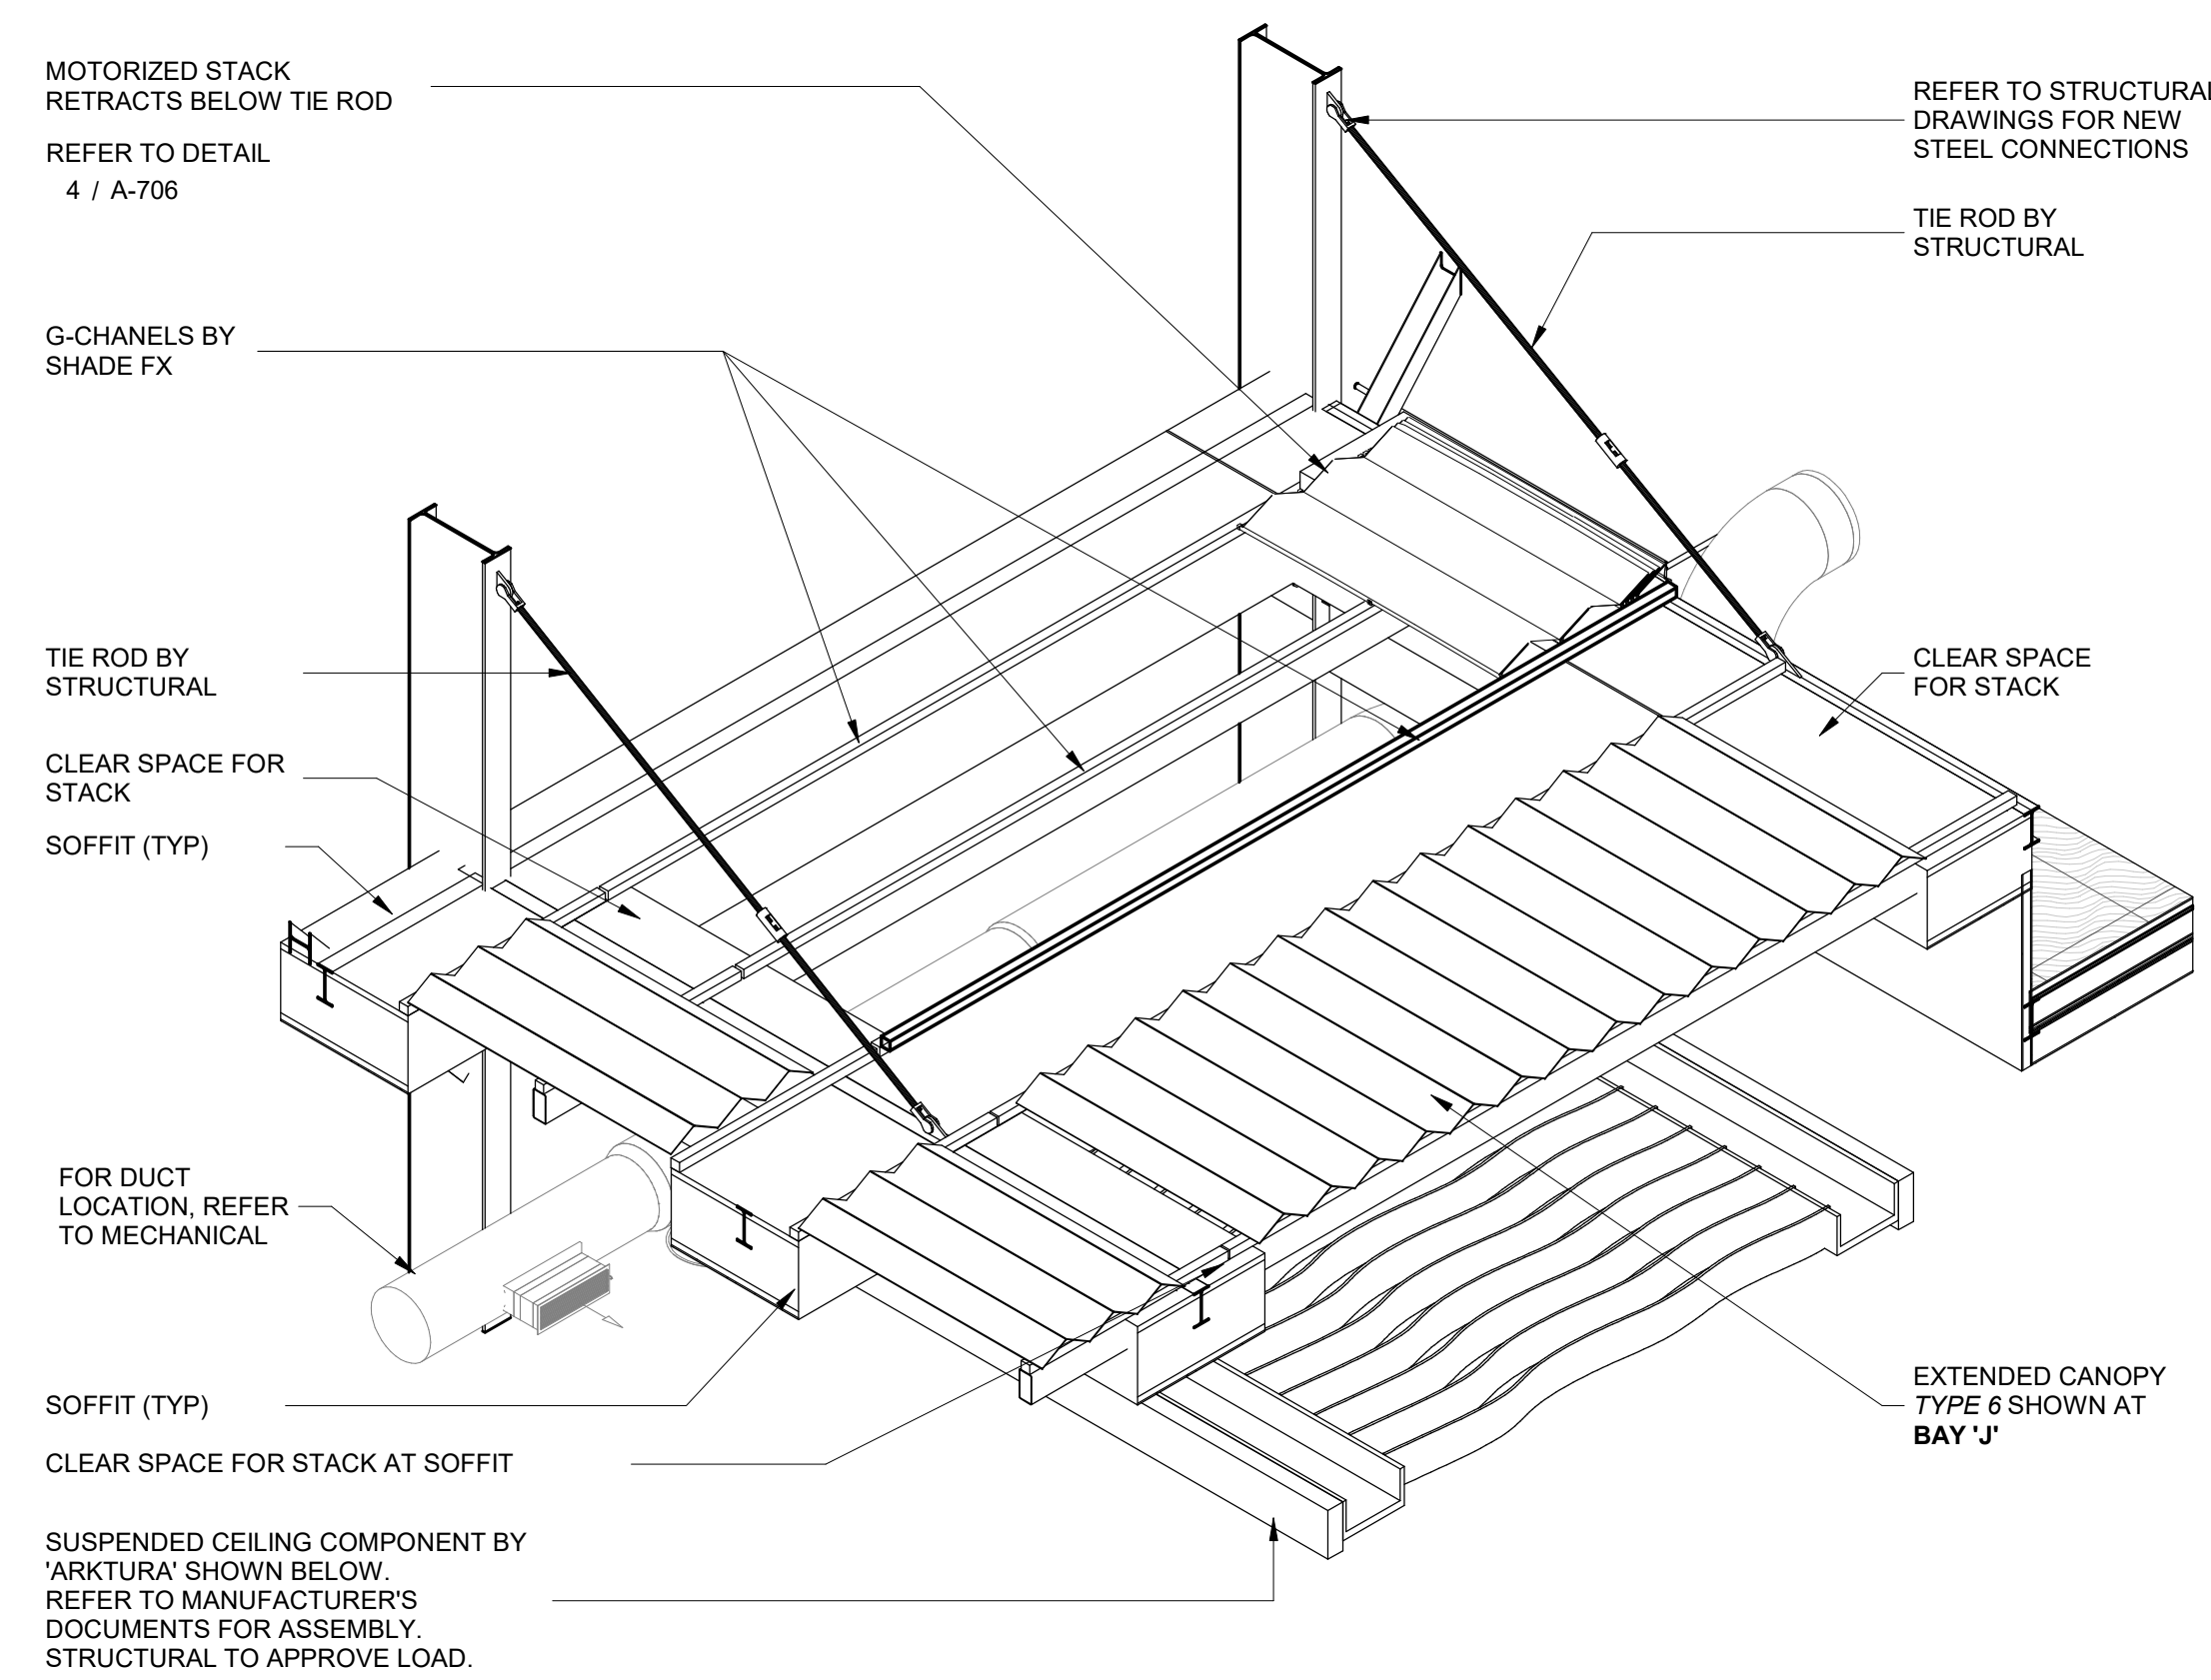

DETAIL ISOMETRIC - SHADEFX RETRACTABLE CANOPY


10
A-705

SCALE: 3/8" = 1'-0"

DETAIL - SECTION - RETRACTABLE CANOPY - LENGTH TYPE 2 AND TYPE 4

9
A-705


SCALE: 3/8" = 1'-0"

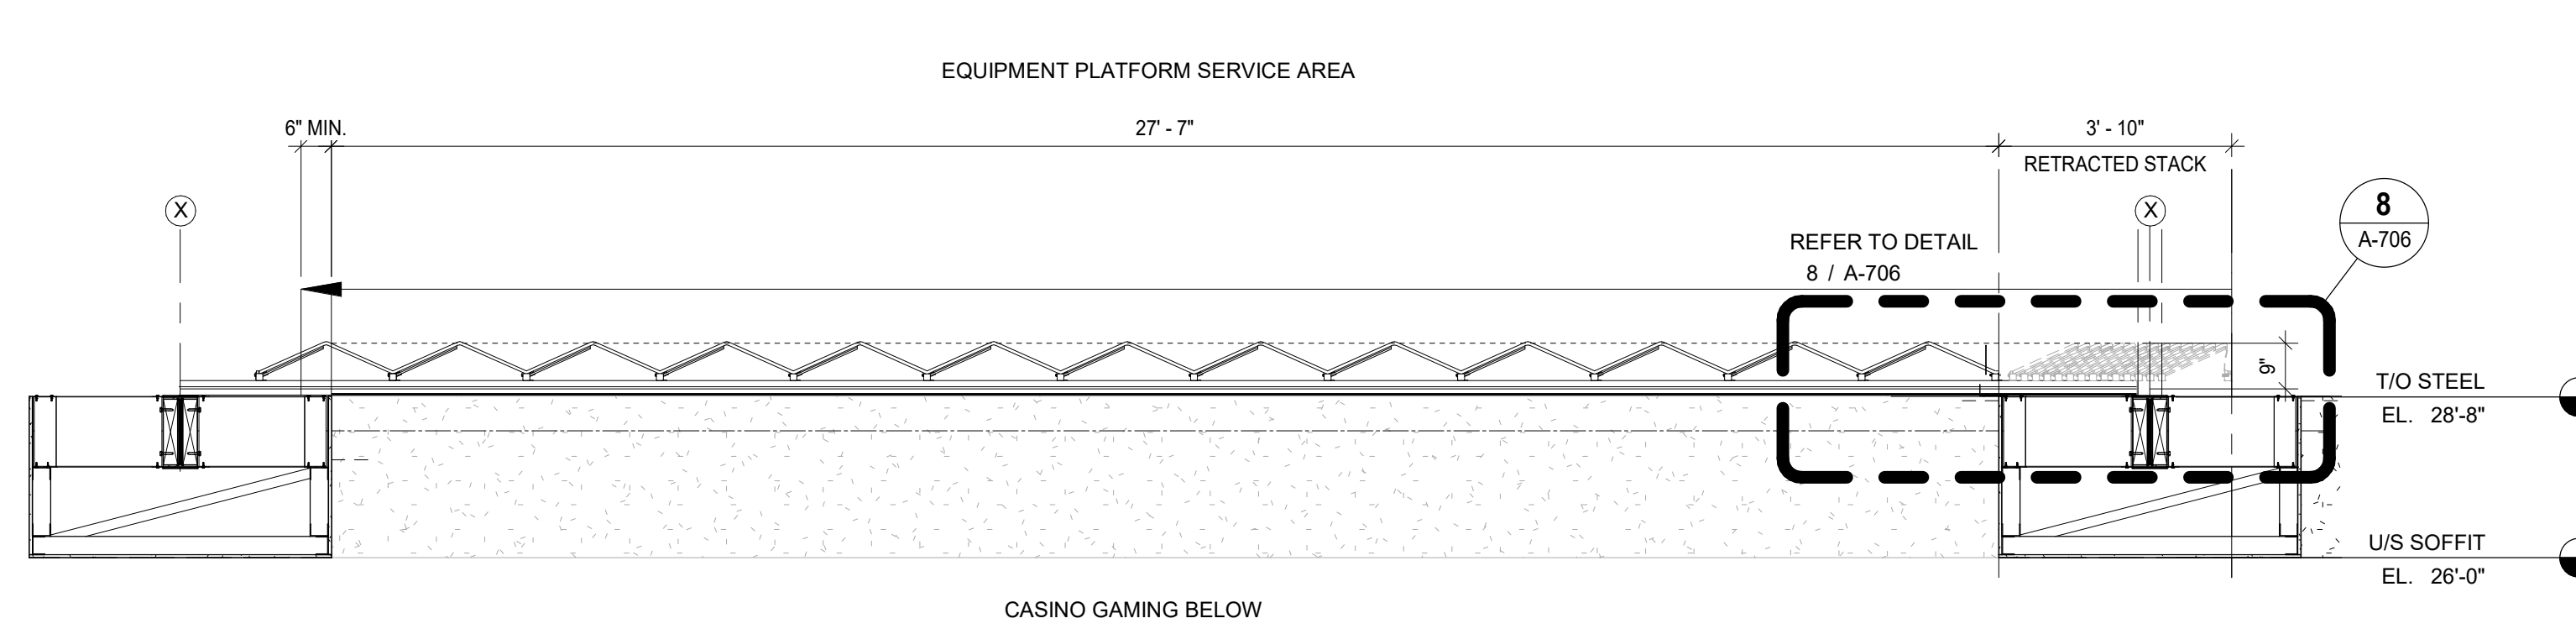

DETAIL - SECTION - RETRACTABLE CANOPY - LENGTH TYPE 1 AND TYPE 3

7
A-705


SCALE: 3/8" = 1'-0"

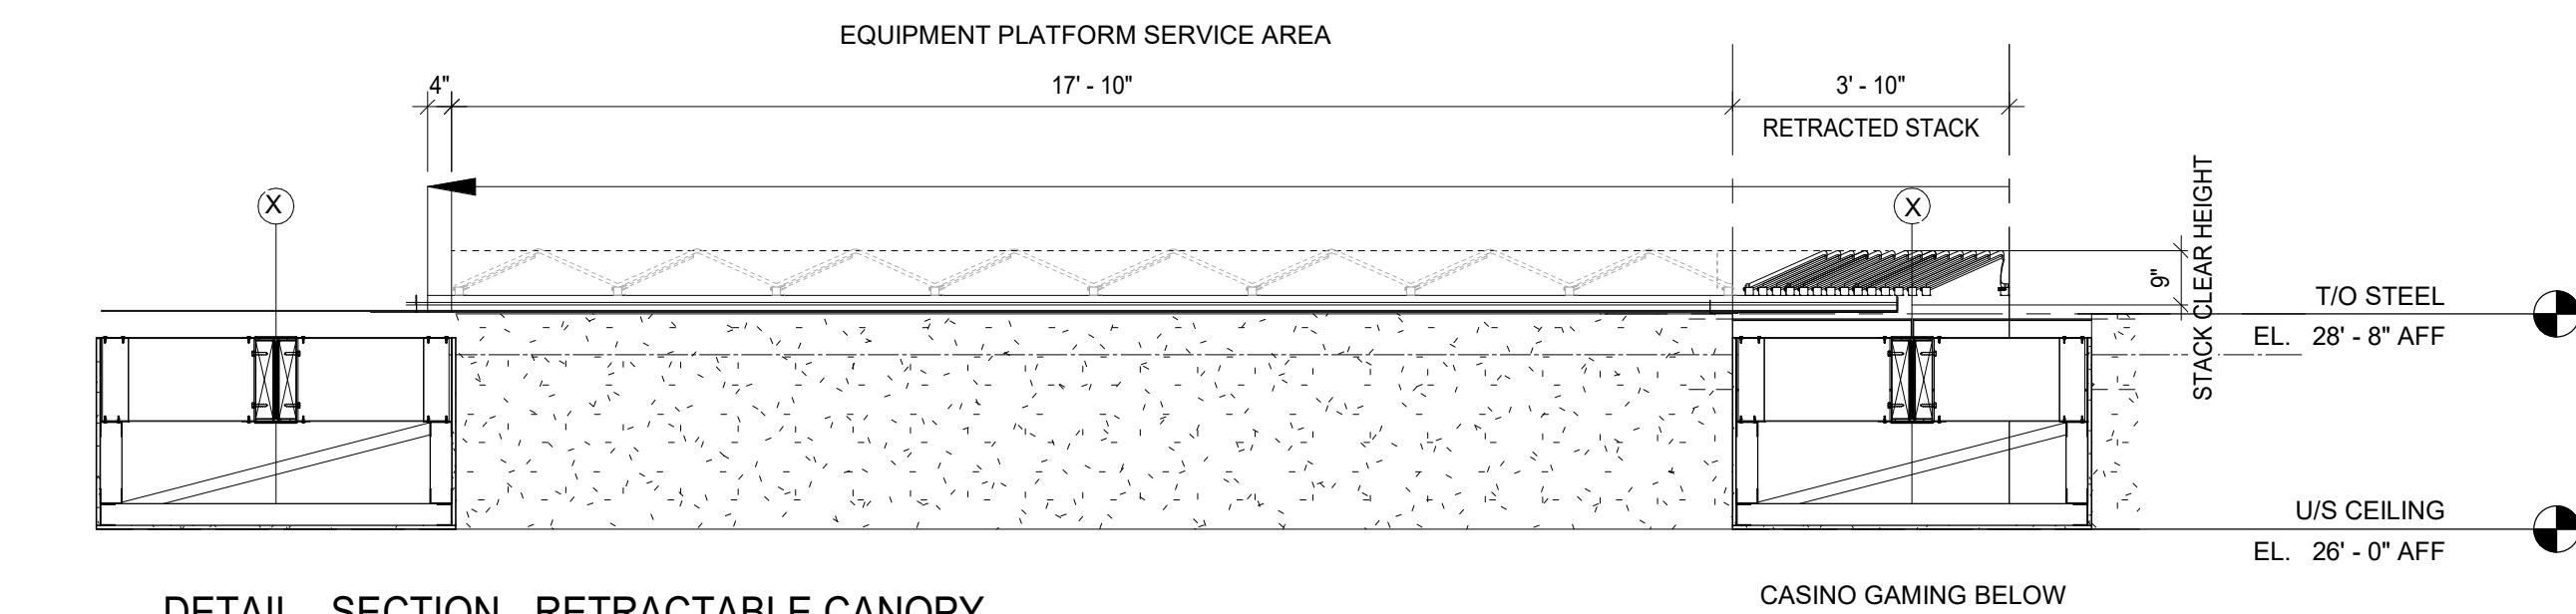

DETAIL - SECTION - RETRACTABLE CANOPY - WIDTH TYPE 3 AND TYPE 4

8
A-705



SCALE: 3/8" = 1'-0"

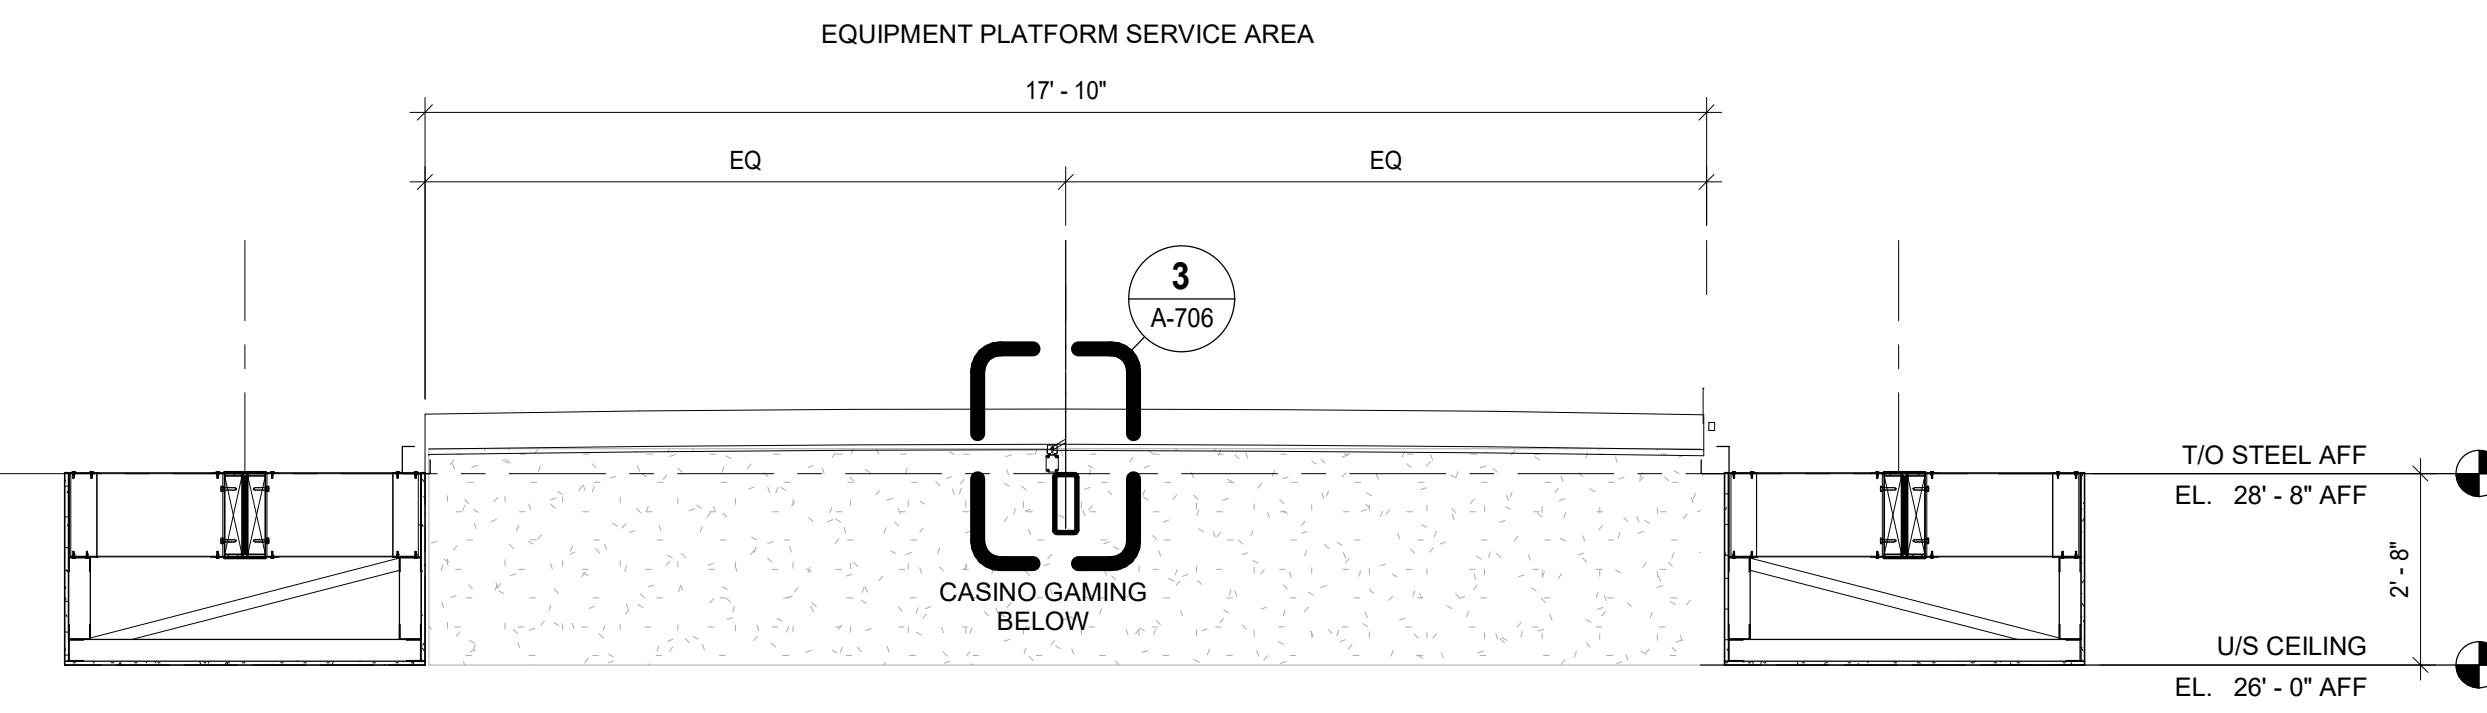

DETAIL - SECTION - RETRACTABLE CANOPY - WIDTH TYPE 1 AND TYPE 2

6
A-705


SCALE: 3/8" = 1'-0"

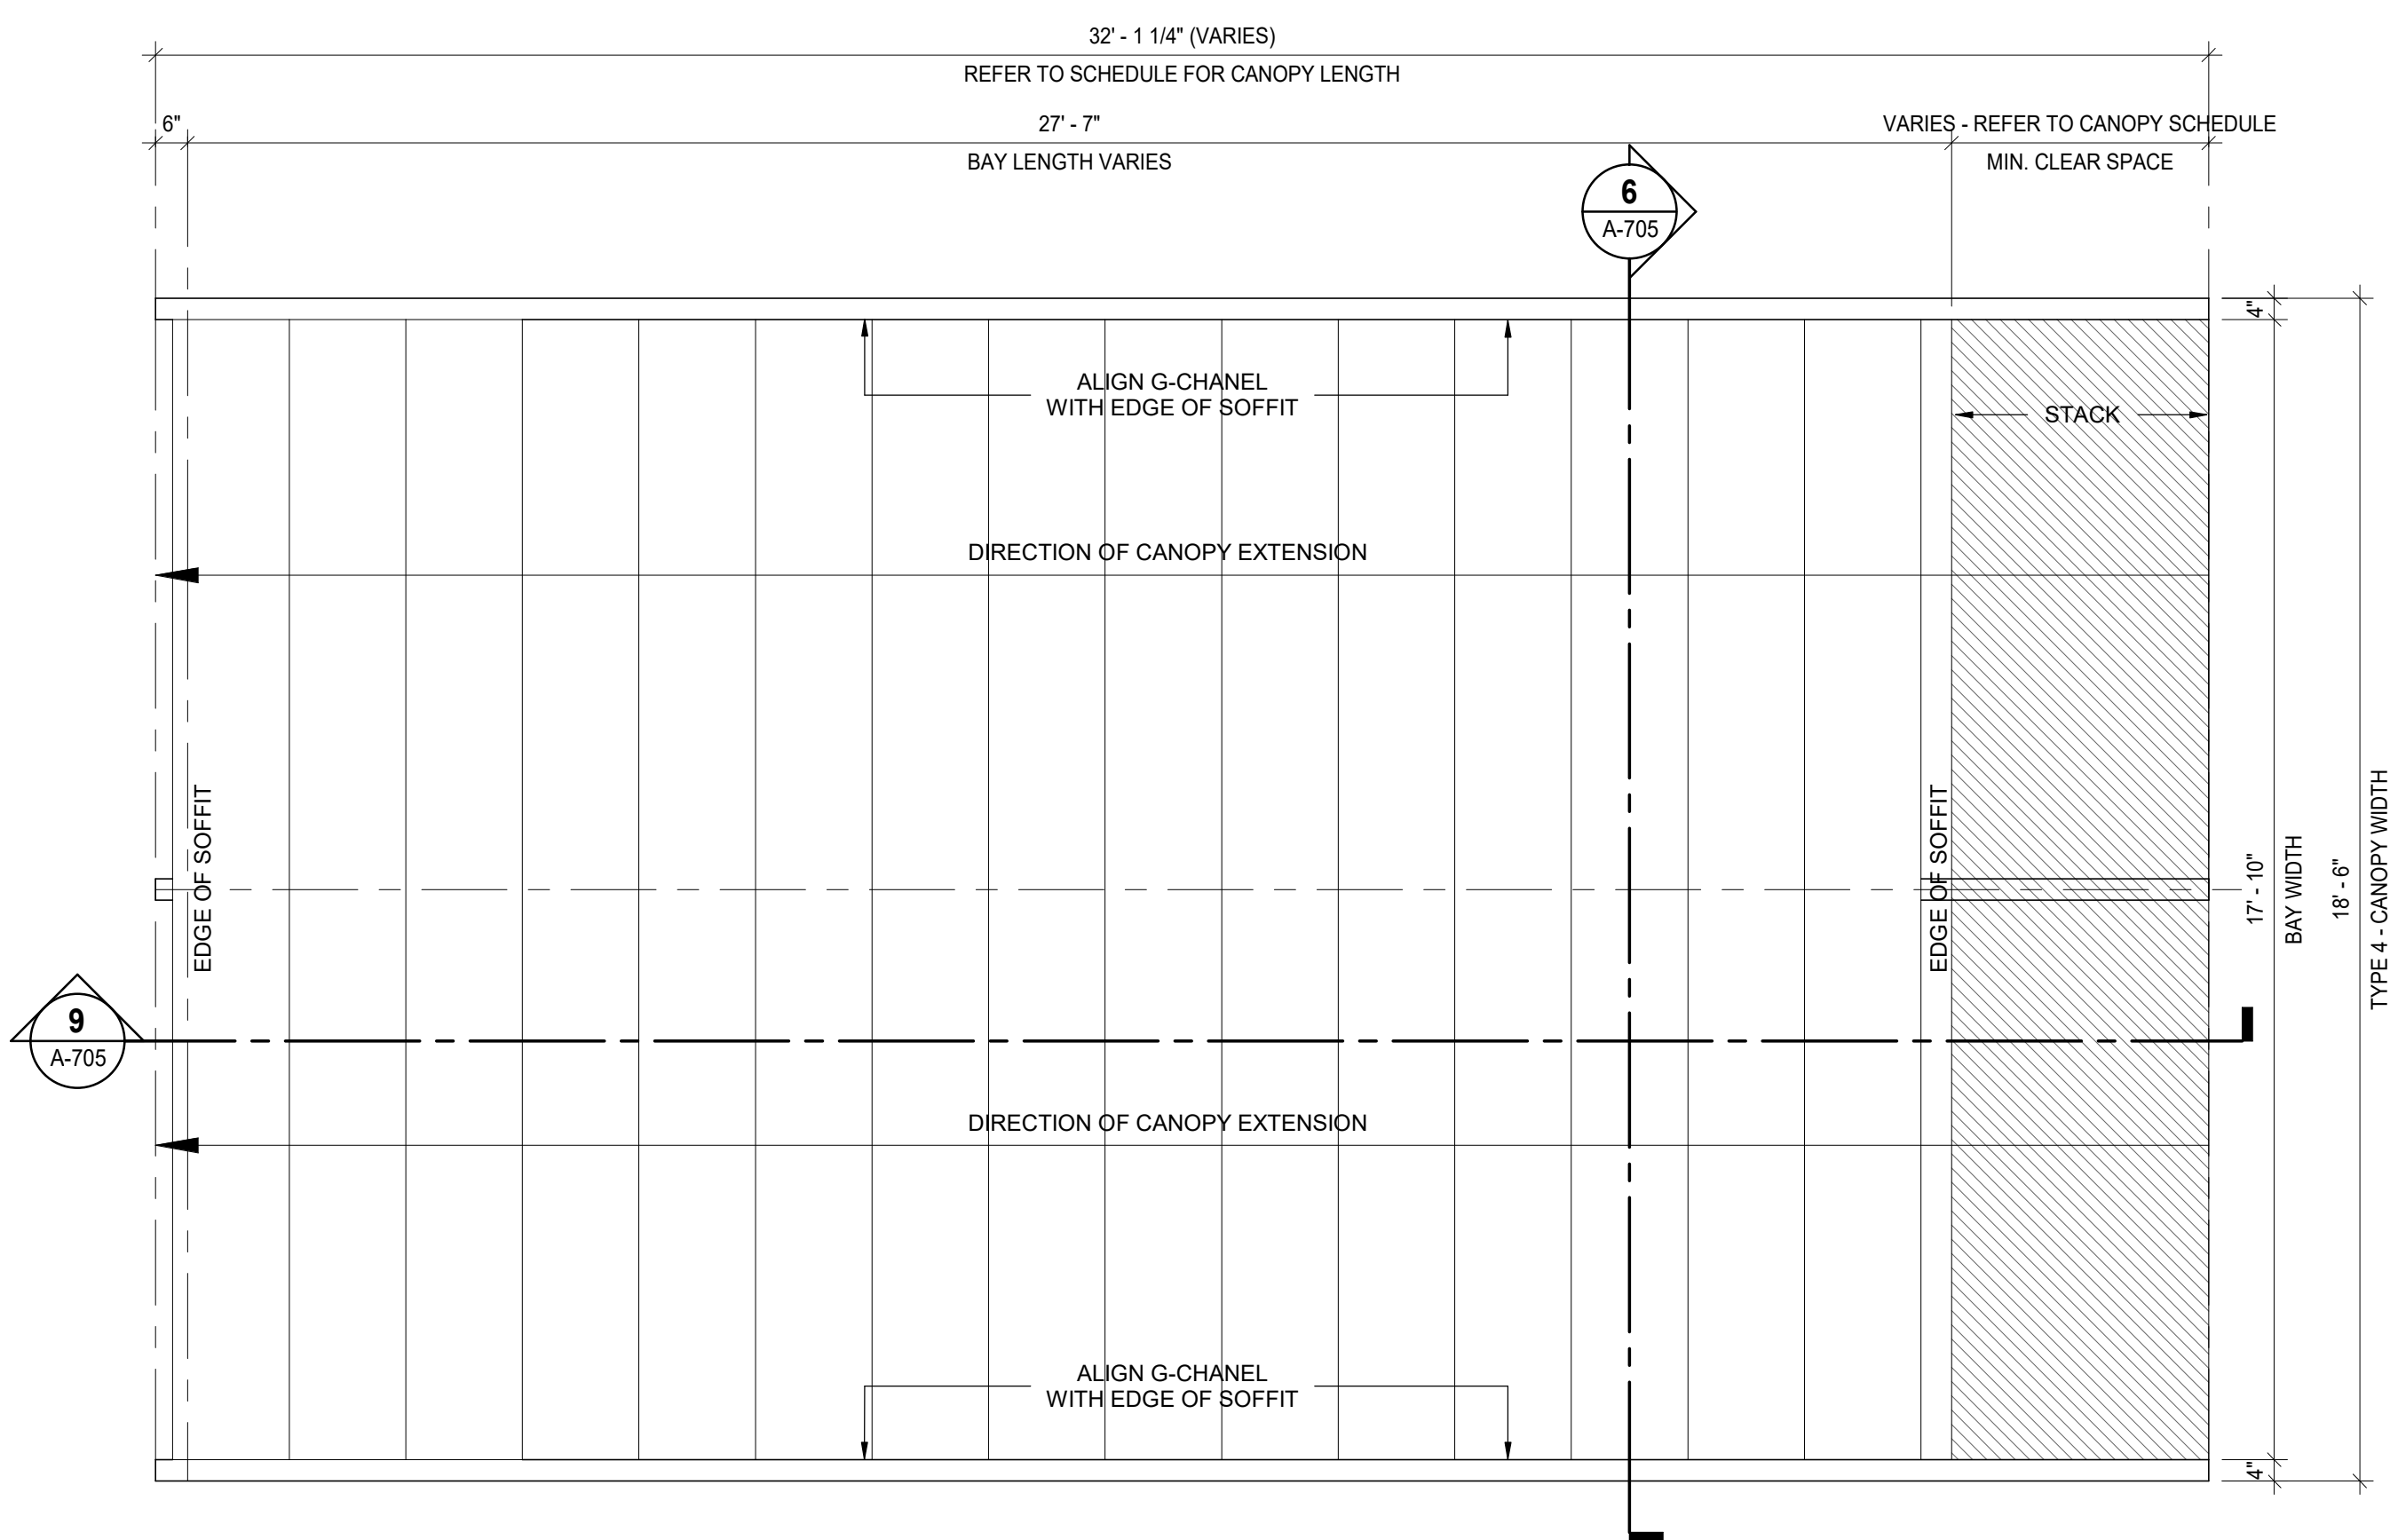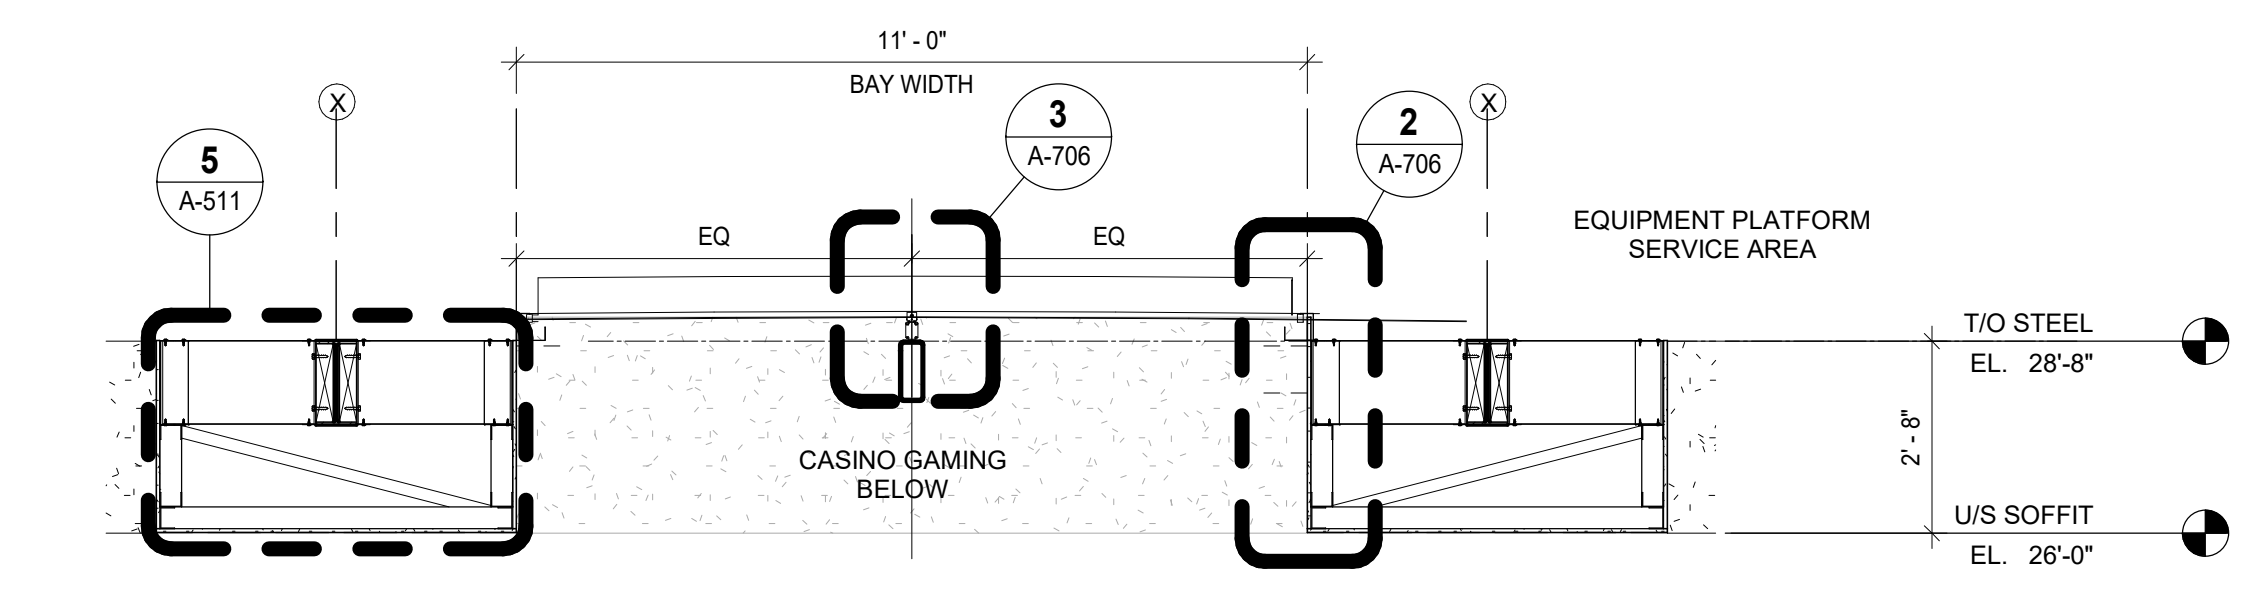

DETAIL - PLAN - SHADEFX CANOPY - TYPES 3, 4 & 6

5
A-705


SCALE: 3/8" = 1'-0"

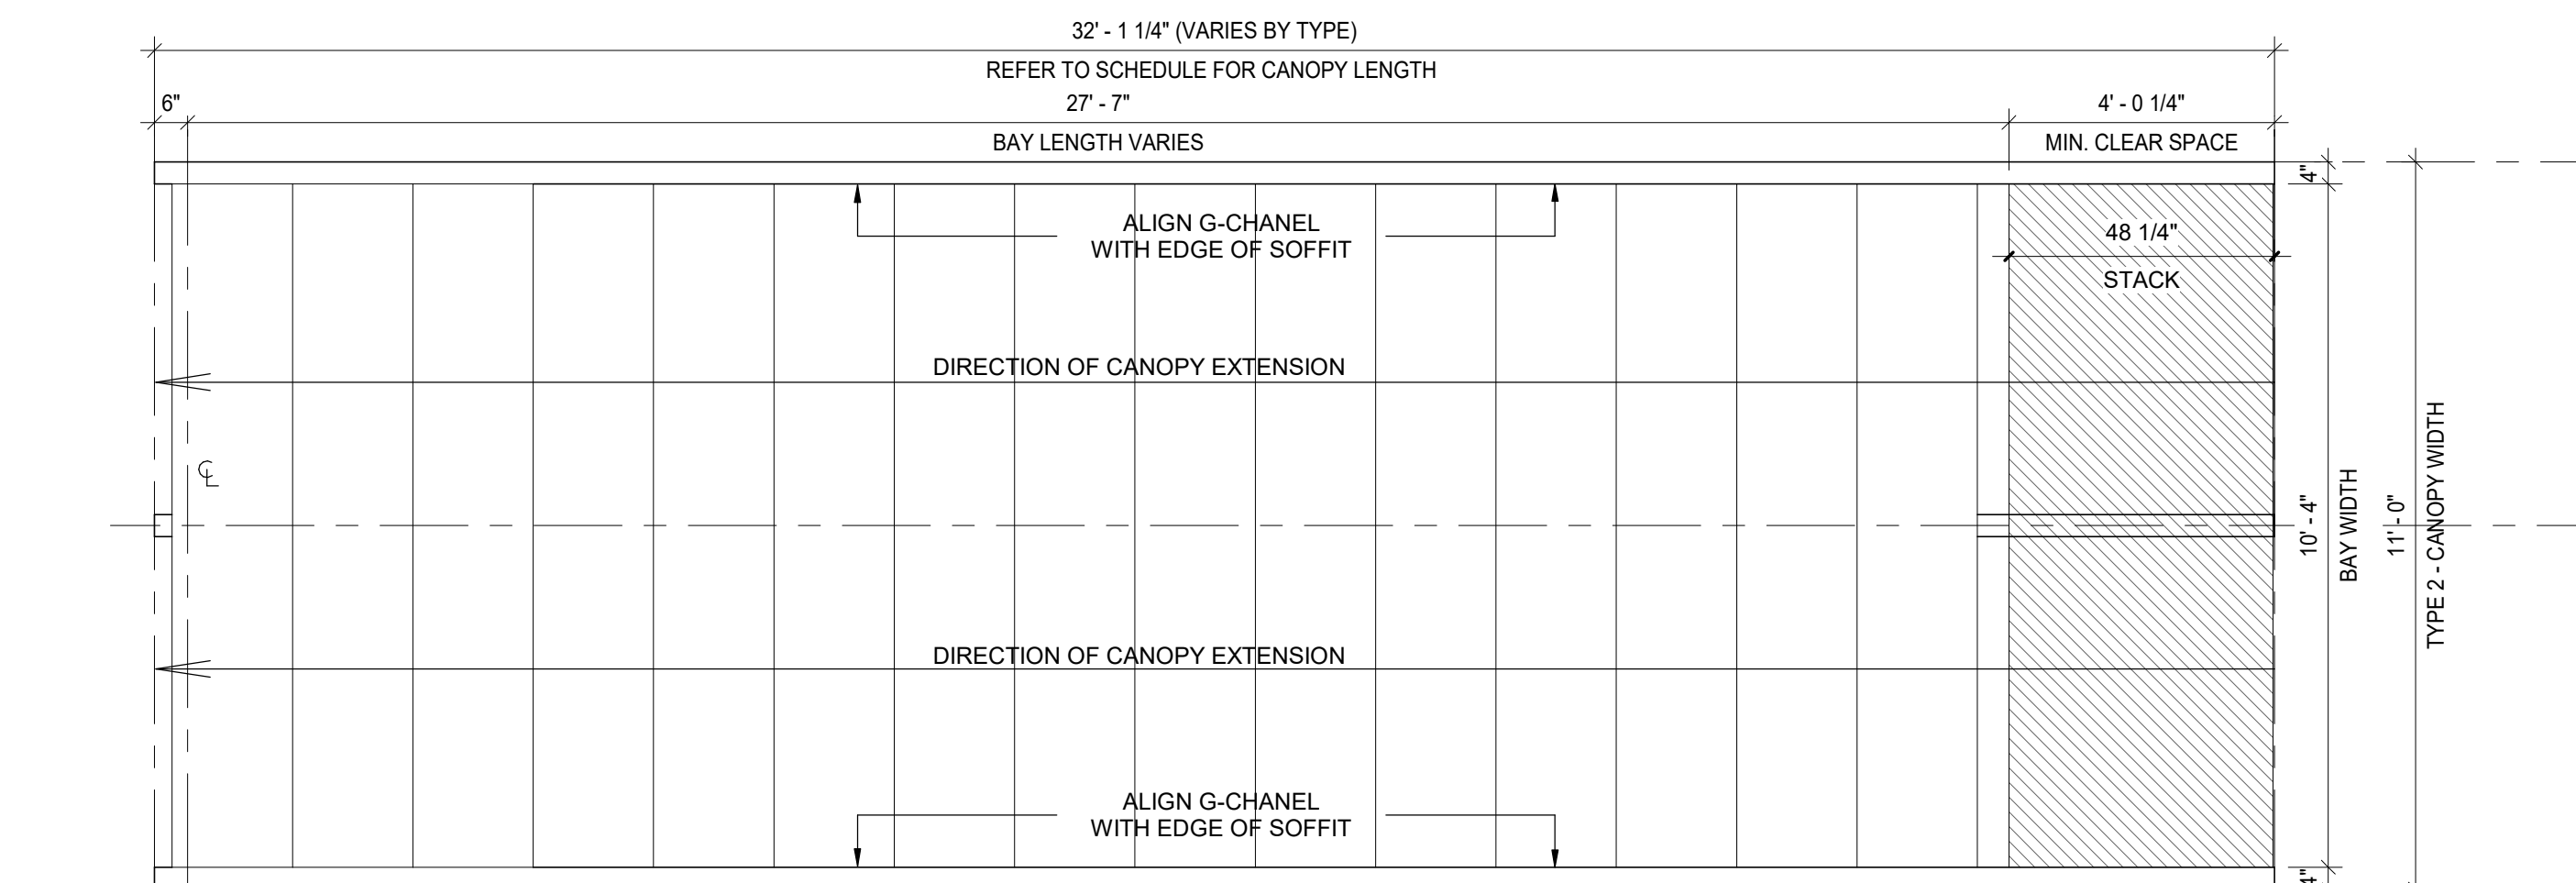

DETAIL - PLAN DIAGRAM - CANOPY TYPES 2 & 5

4
A-705


SCALE: 3/8" = 1'-0"

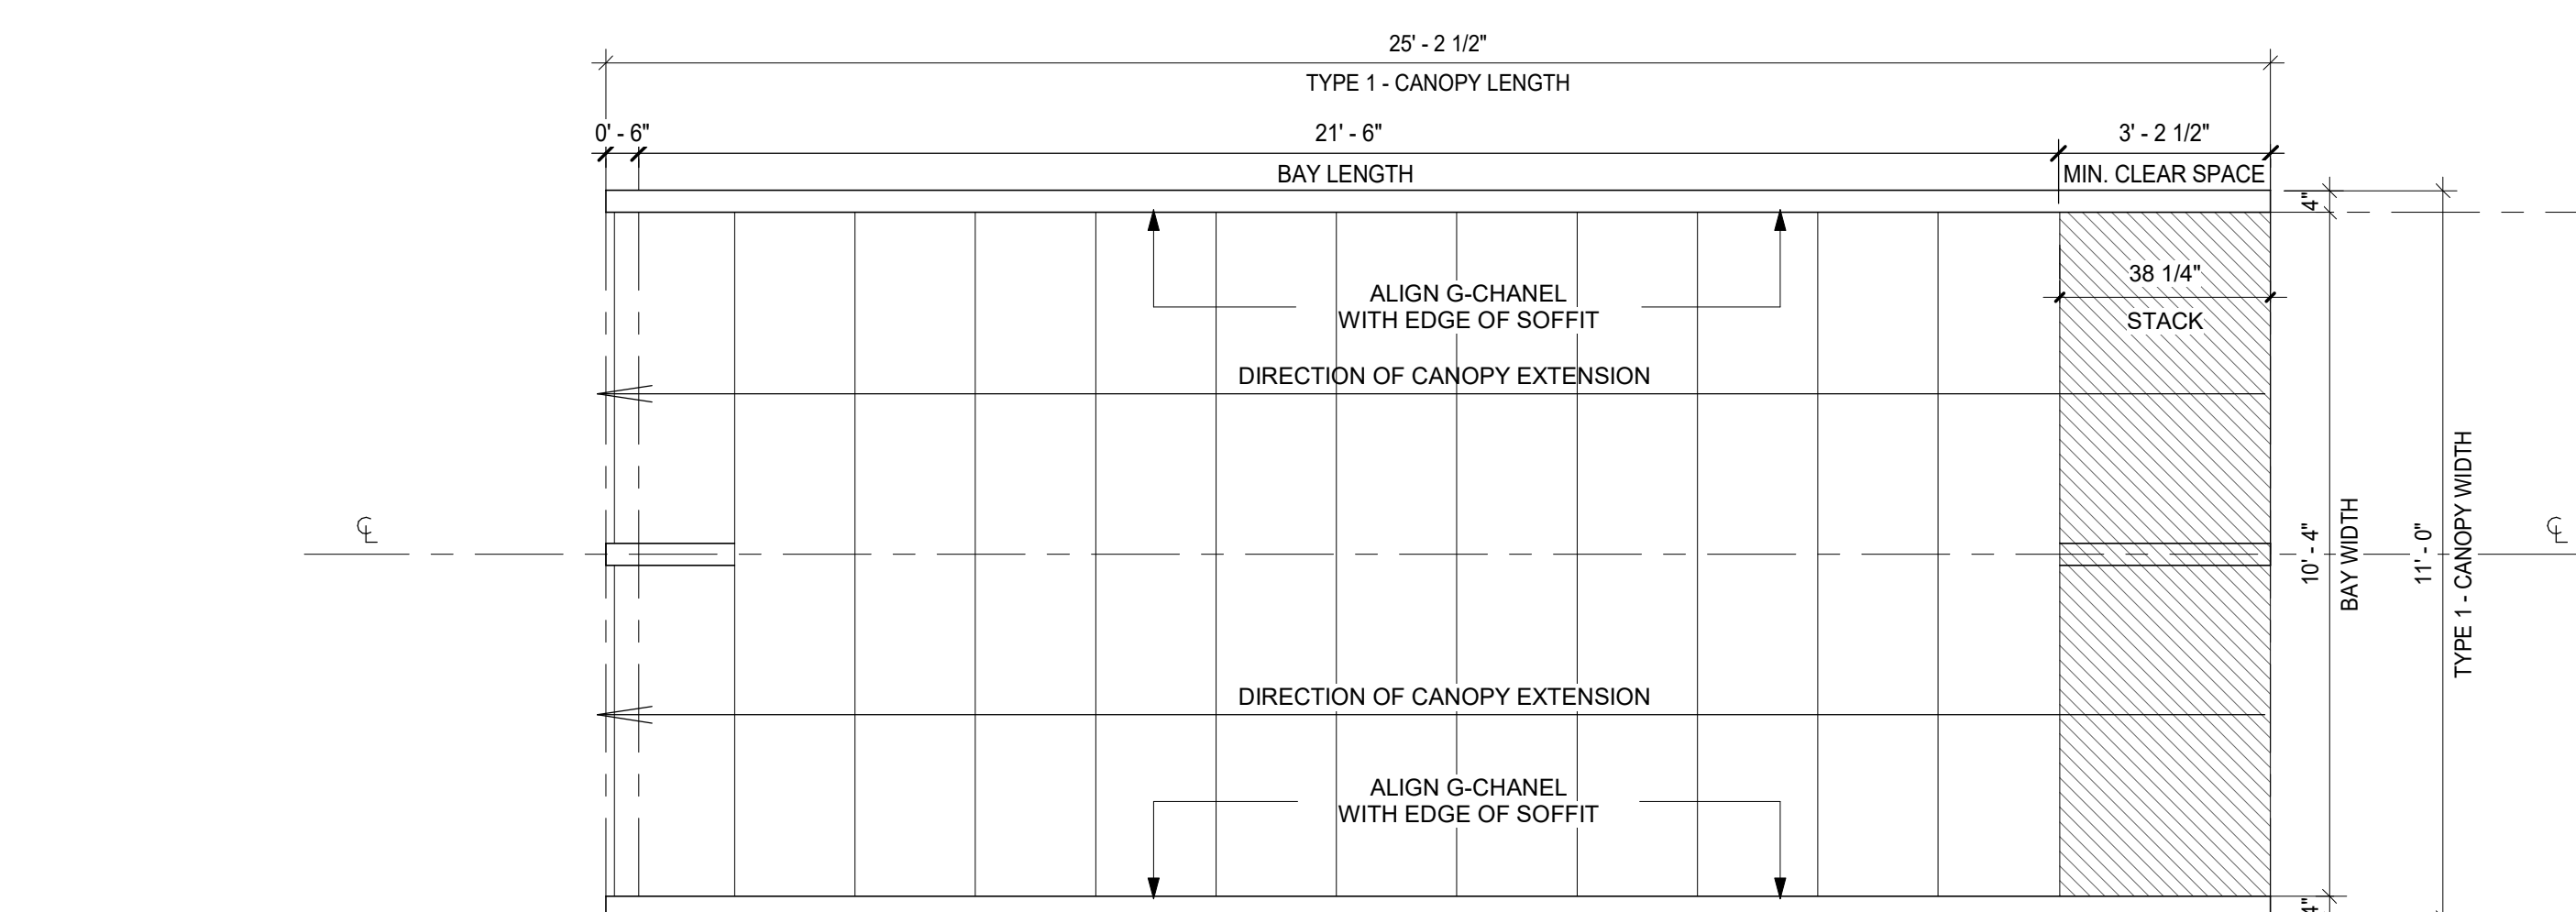

DETAIL - PLAN DIAGRAM - CANOPY TYPE 1

3
A-705


SCALE: 3/8" = 1'-0"

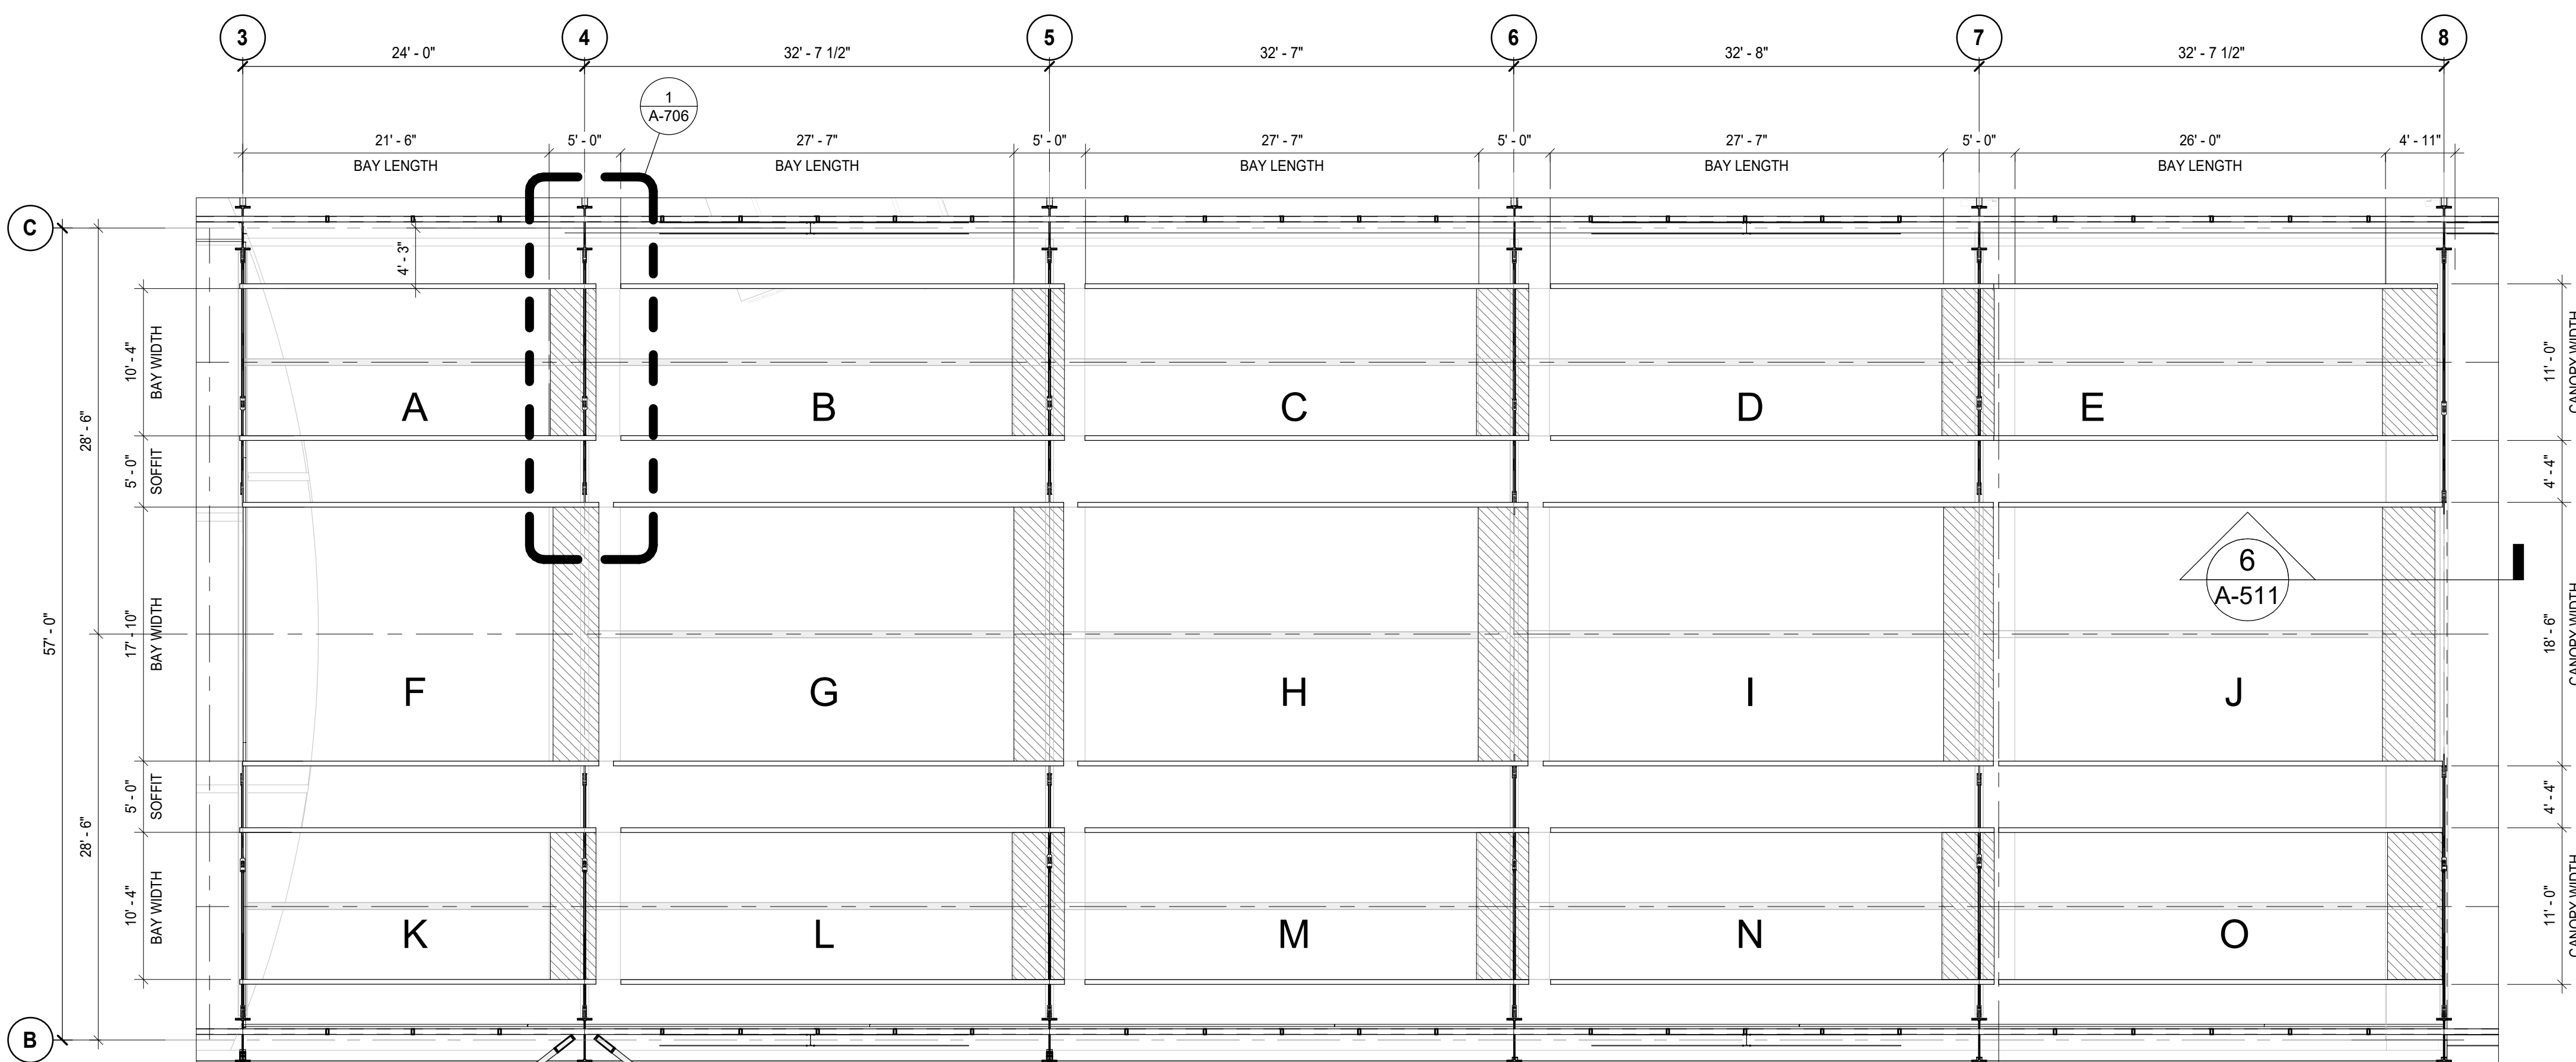

KEYPLAN - CANOPIES RETRACTED (NIGHT MODE)

2
A-705

SCALE: 1/8" = 1'-0"

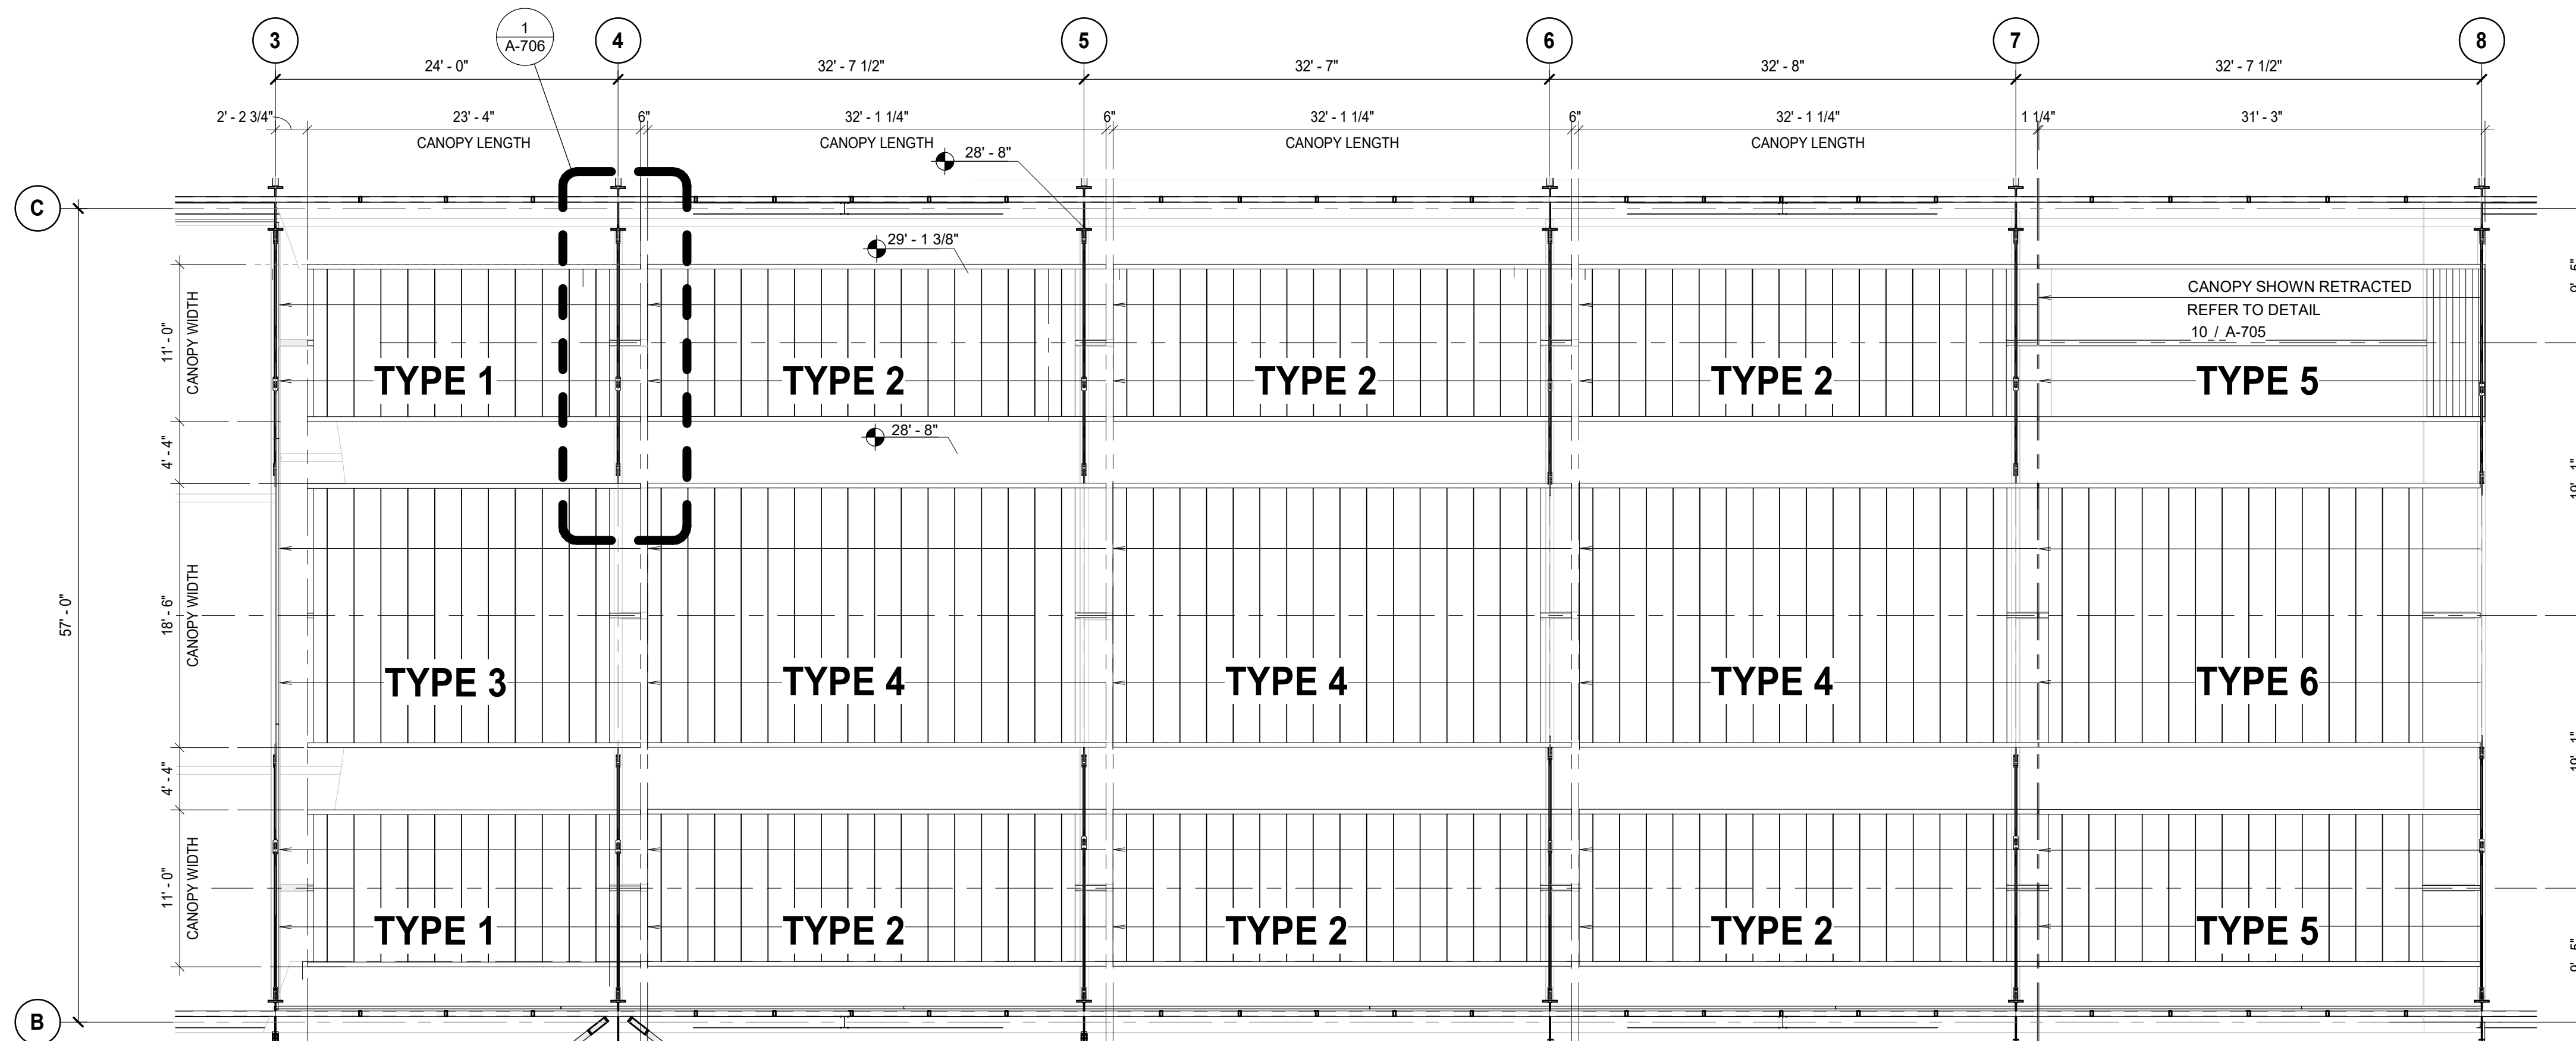

KEYPLAN - CANOPIES EXTENDED (DAY MODE)

1
A-705

SCALE: 1/8" = 1'-0"

SHADE FX RETRACTABLE CANOPY SCHEDULE							
BAY IDENTITY	BAY LENGTH (FT.)	BAY WIDTH (FT.)	CANOPY TYPE	STACK CLEARANCE (FT.)	CANOPY LENGTH (FT.)	CANOPY WIDTH (FT.)	Manufacturer
A, K	21'-6"	10'-4"	TYPE 1	3'-2 1/4"	23'-4"	11'-0"	ShadeFX
B, C, D, L, M, N	27'-7"	10'-4"	TYPE 2	4'-0 1/4"	31'-11"	11'-0"	ShadeFX
E	21'-6"	17'-10"	TYPE 3	3'-2 1/2"	23'-4"	18'-6"	ShadeFX
G, H, I, J	27'-7"	17'-10"	TYPE 4	4'-0 1/4"	31'-11"	18'-6"	ShadeFX
O	26'-0"	10'-4"	TYPE 5	3'-10 1/4"	31'-3"	11'-0"	ShadeFX
J	26'-0"	17'-10"	TYPE 6	3'-10 1/4"	31'-3"	18'-6"	ShadeFX