



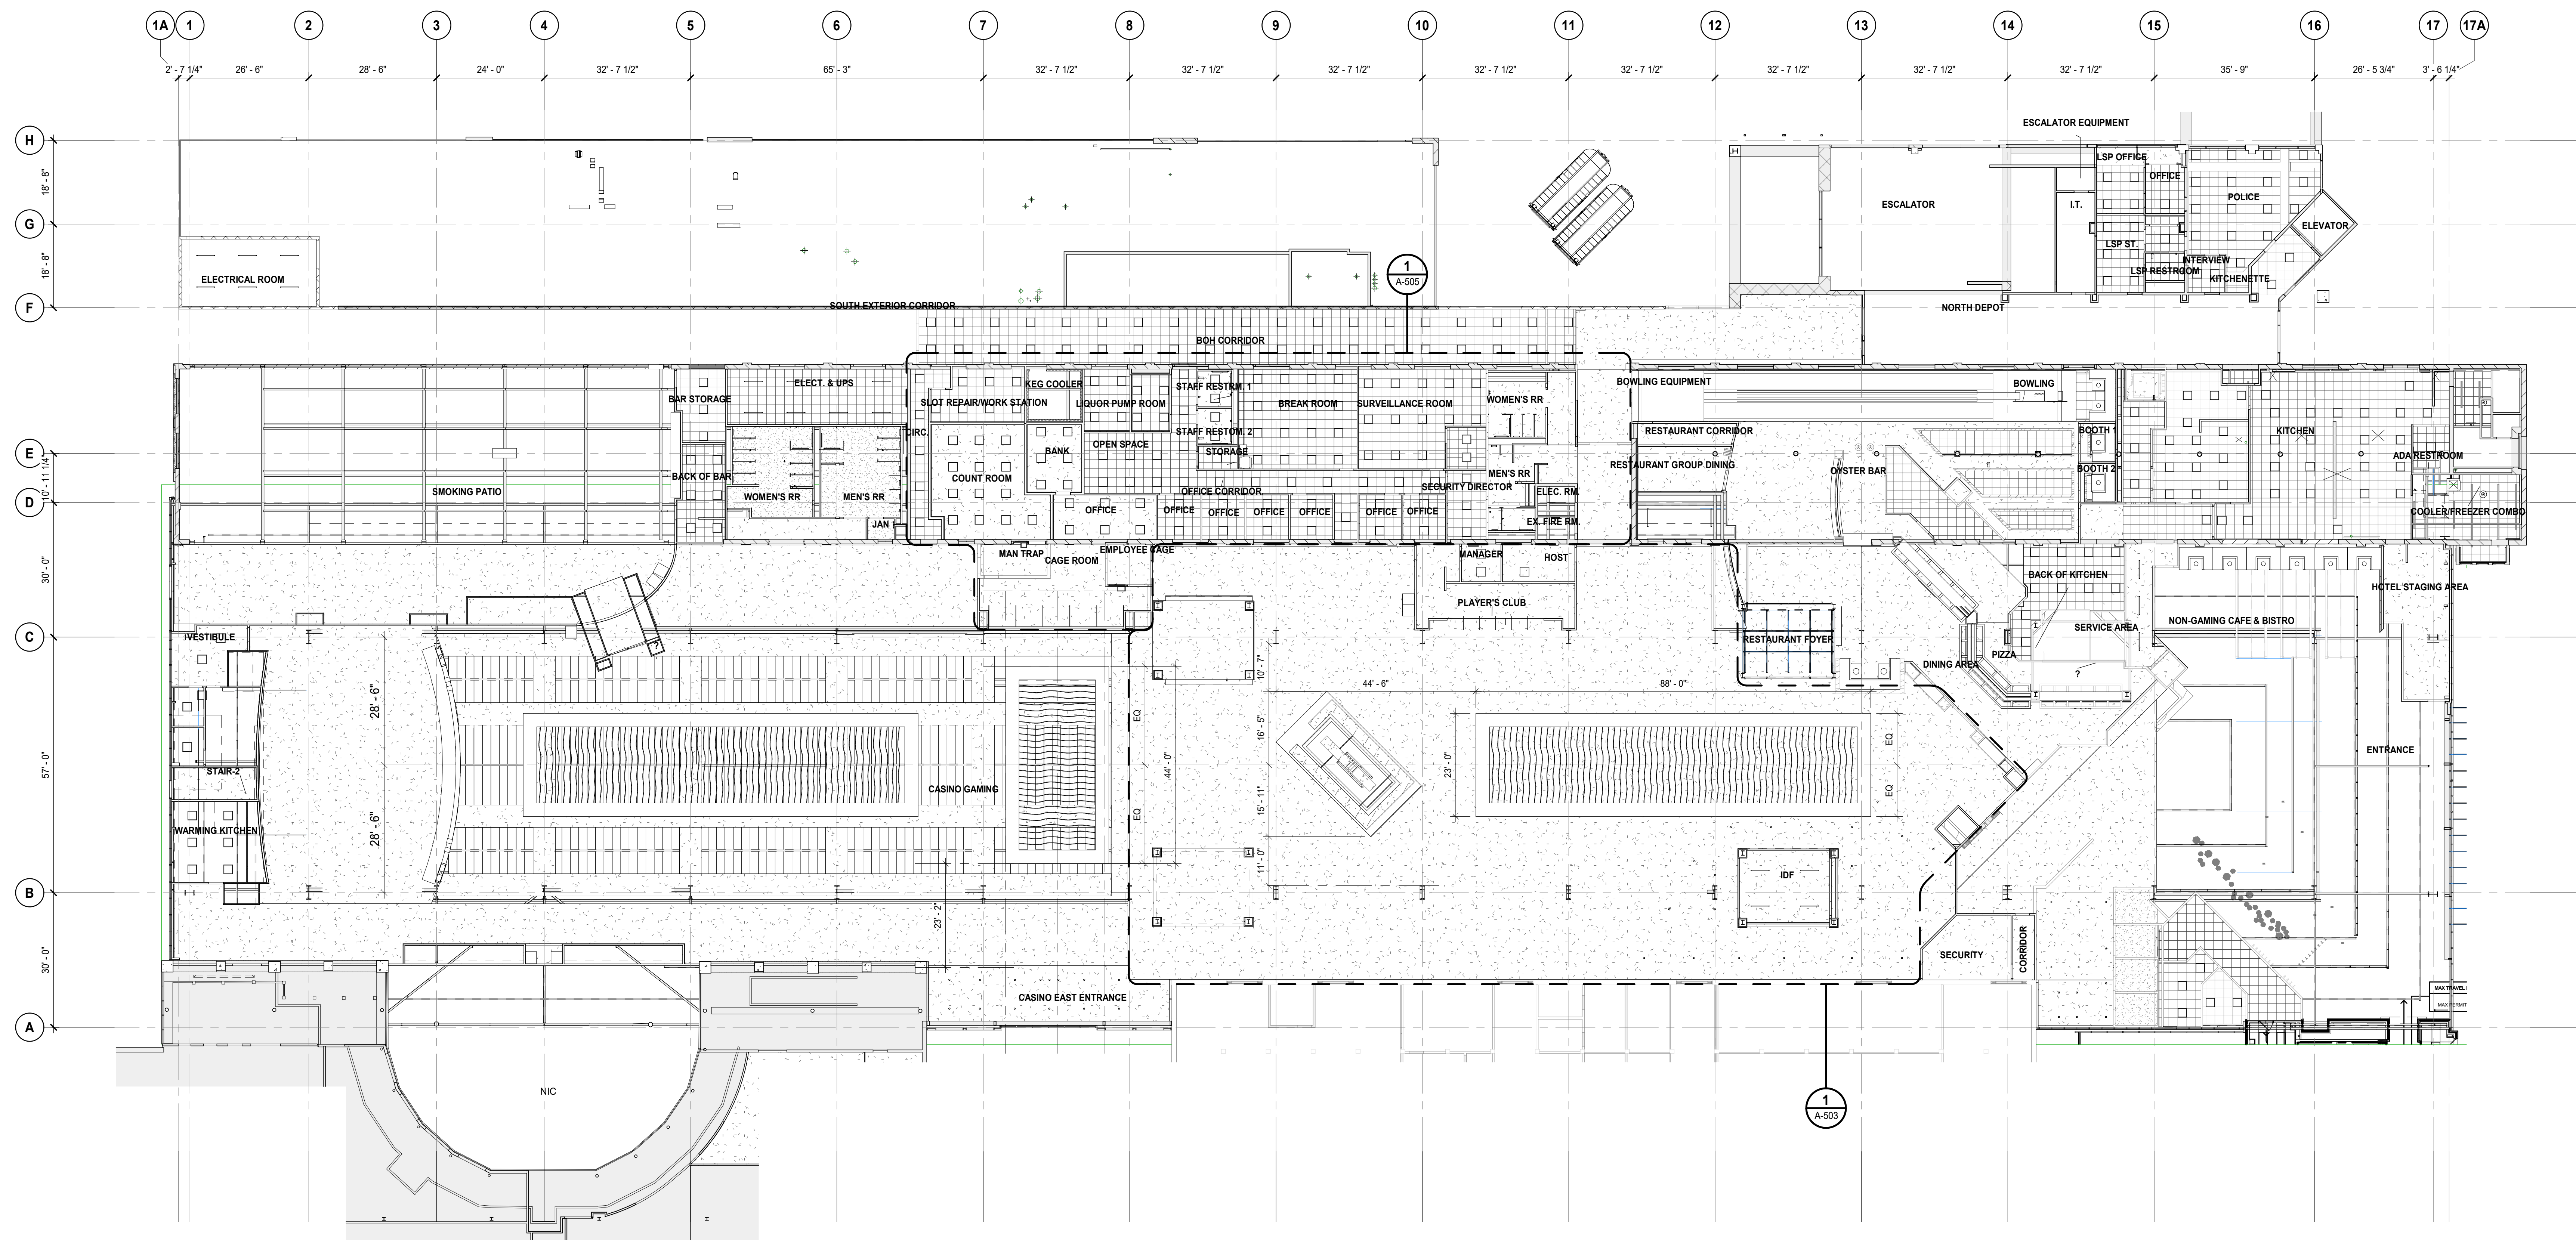

2 REFLECTED CEILING PLAN REFERENCE PLAN
A-500 SCALE: 1/16" = 1'-0"

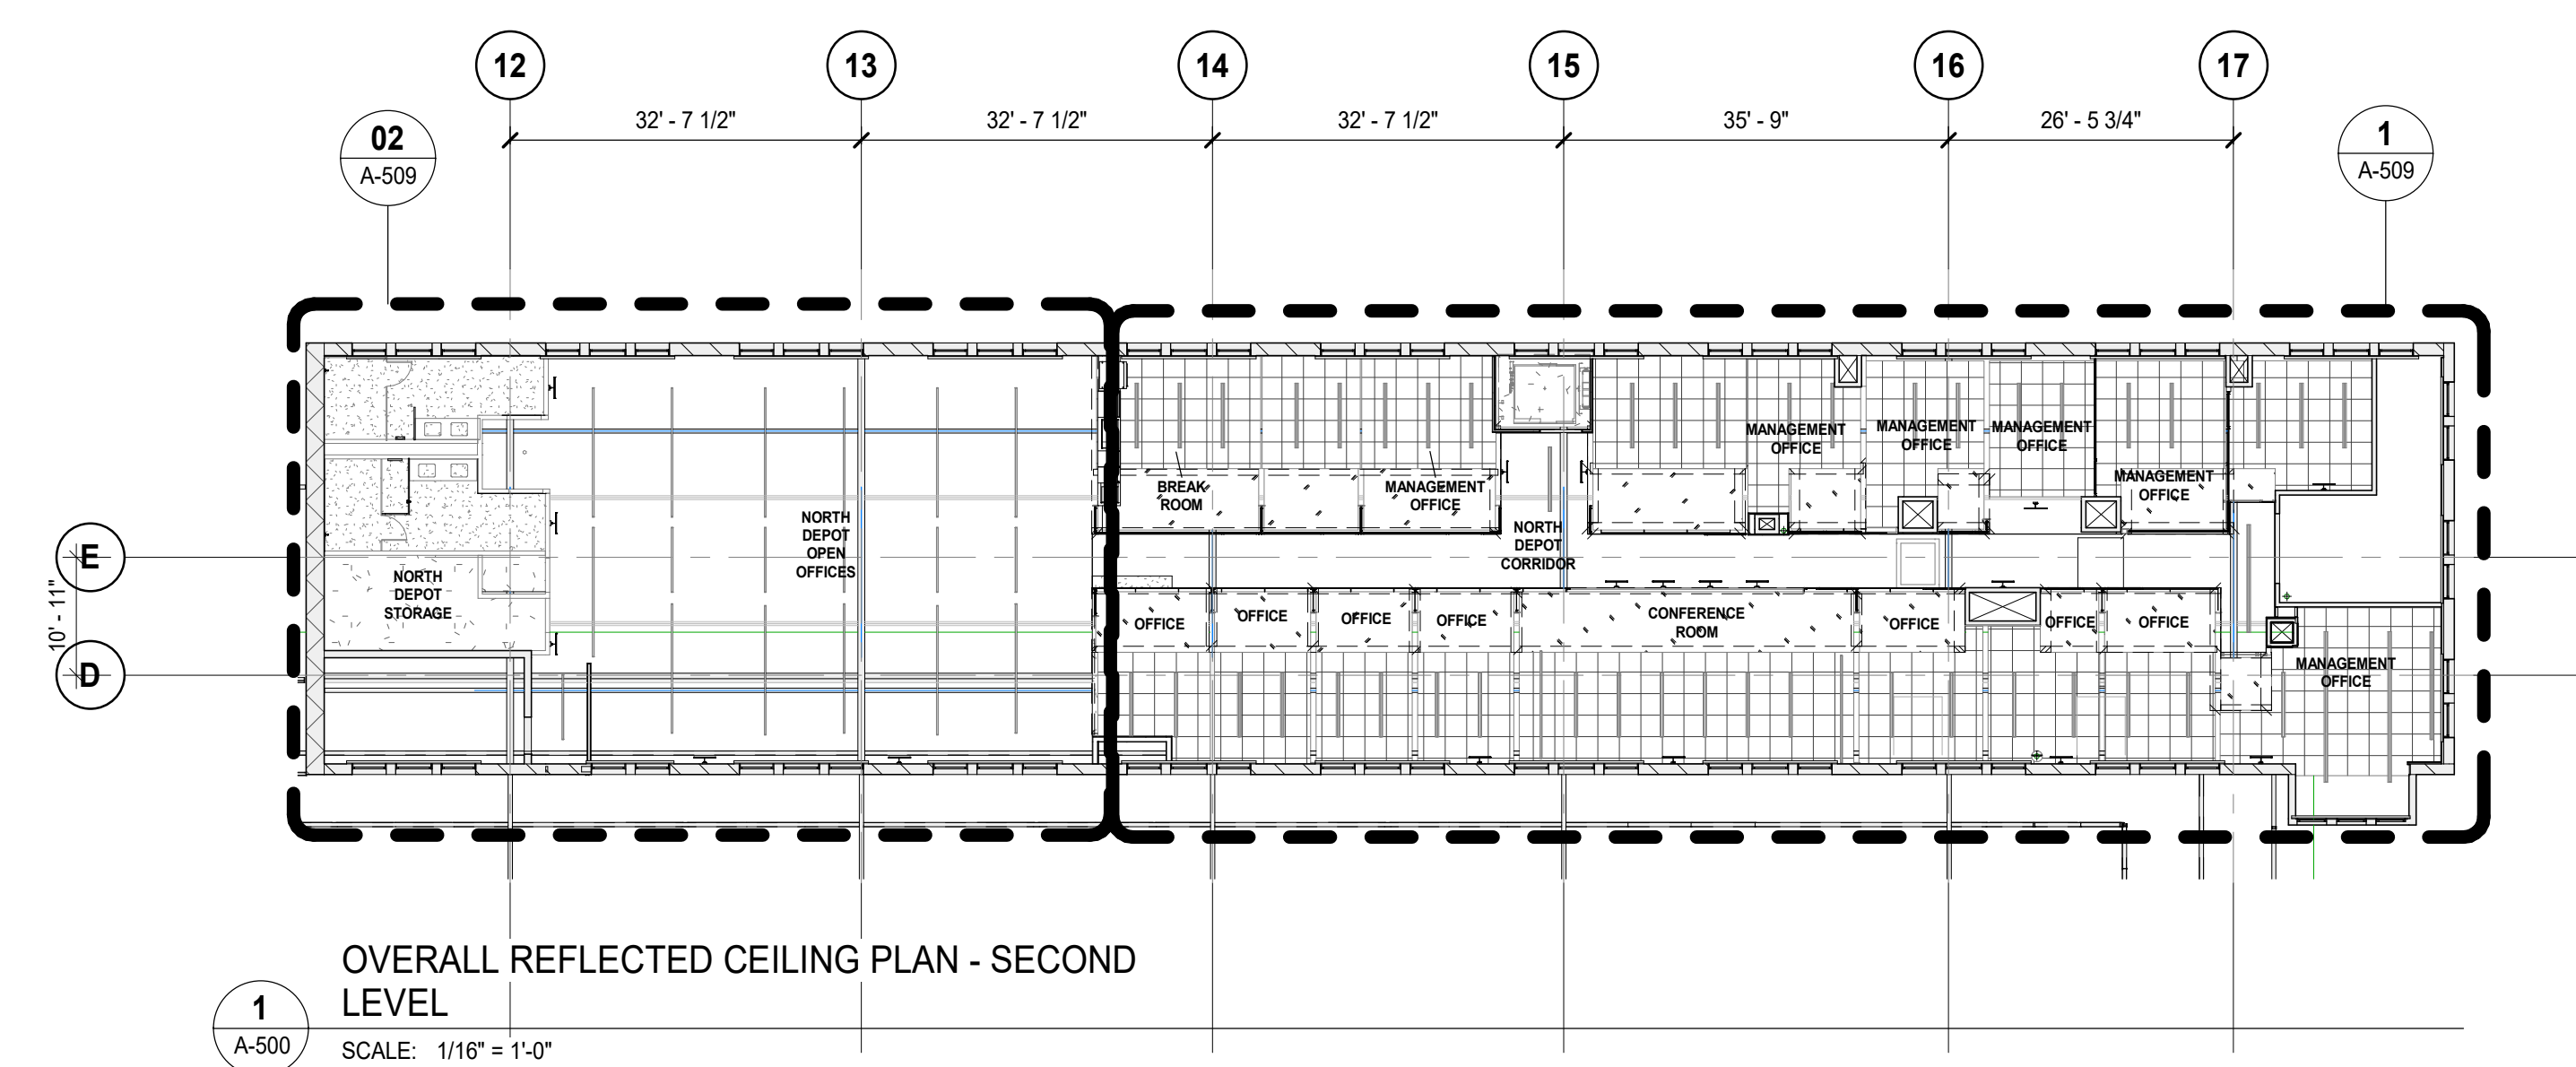

OVERALL REFLECTED CEILING PLAN - SECOND LEVEL
1 A-500 SCALE: 1/16" = 1'-0"