




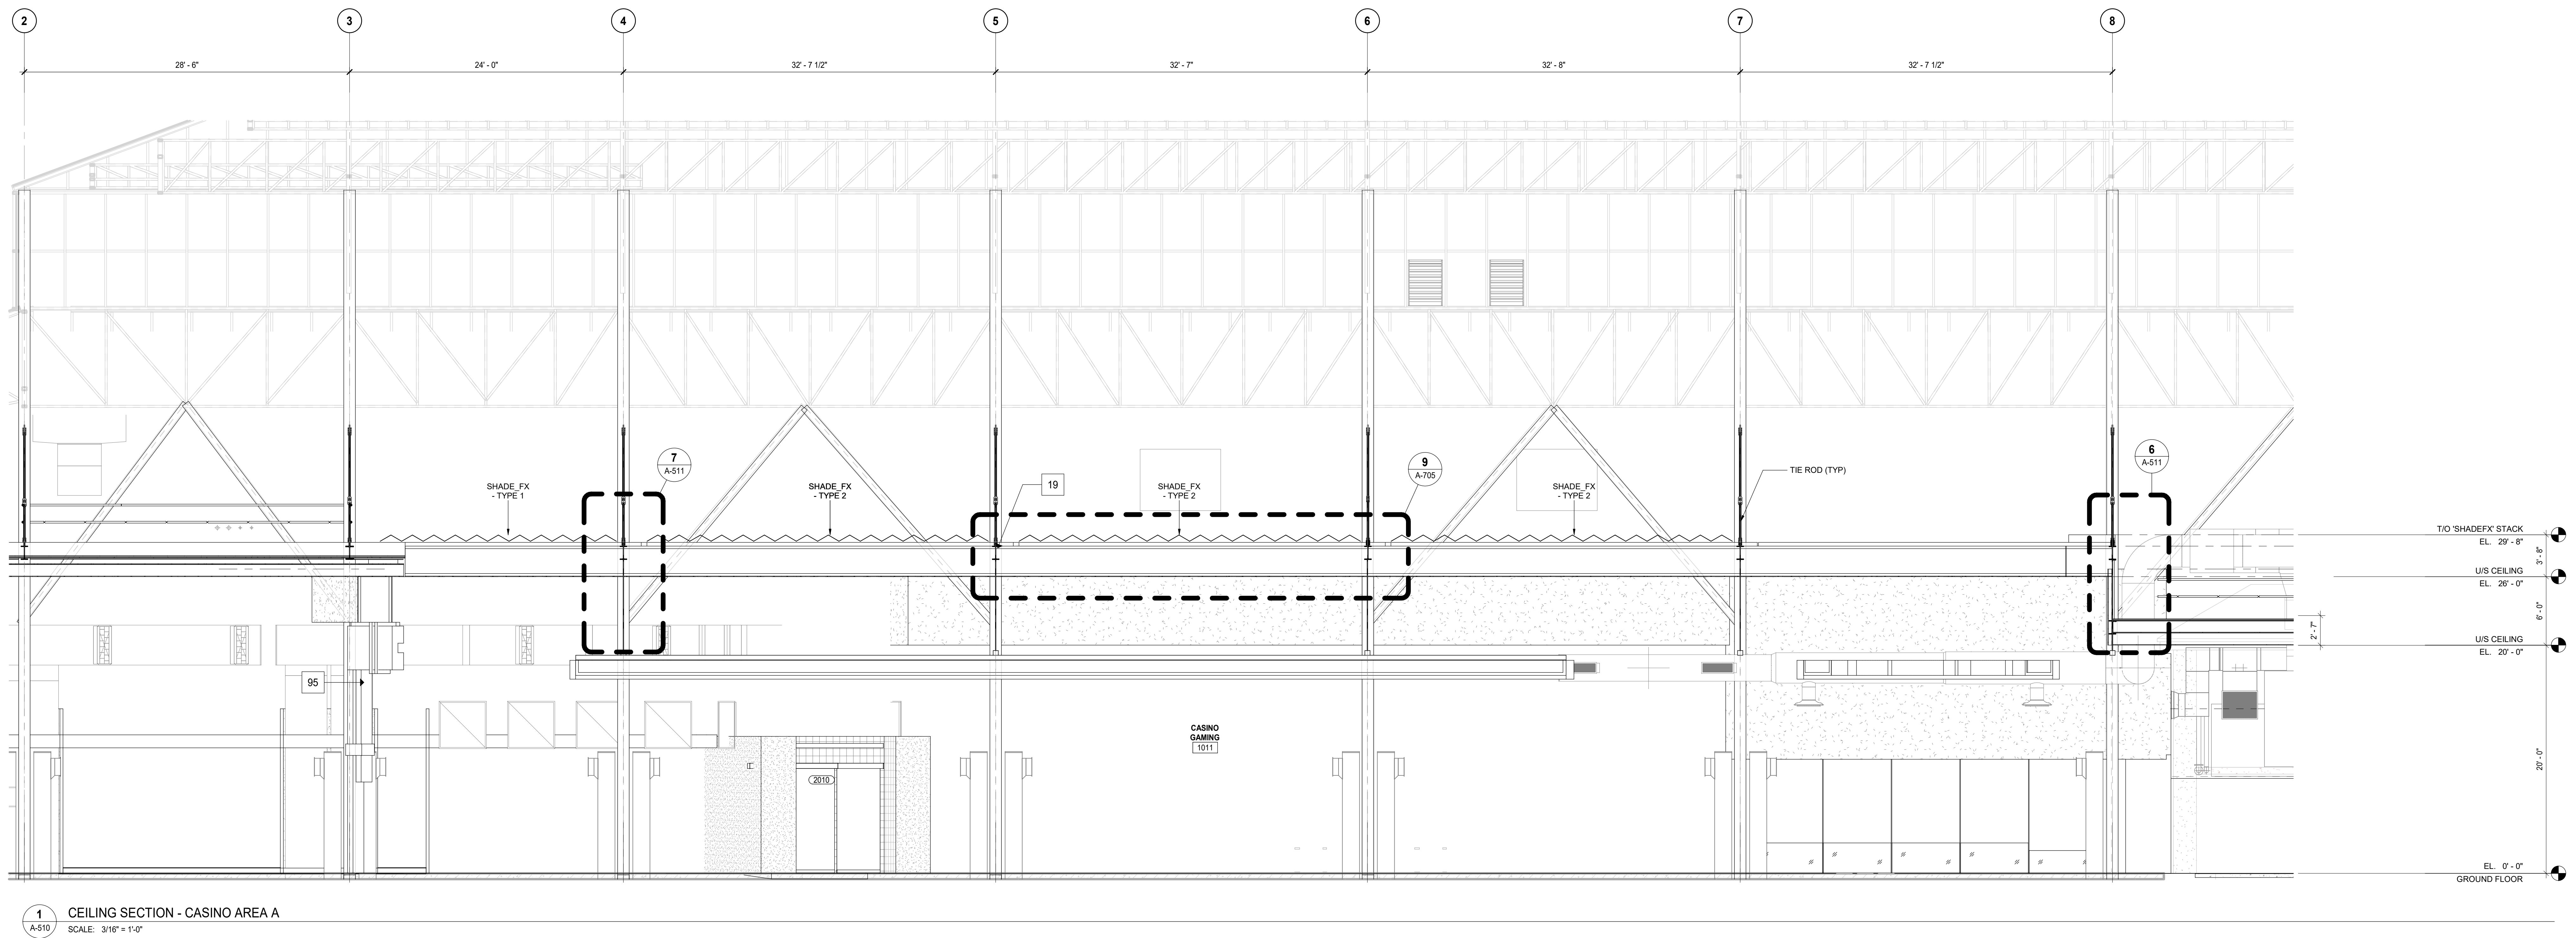

1 CEILING SECTION - CASINO AREA A
SCALE: 3/16" = 1'-0"

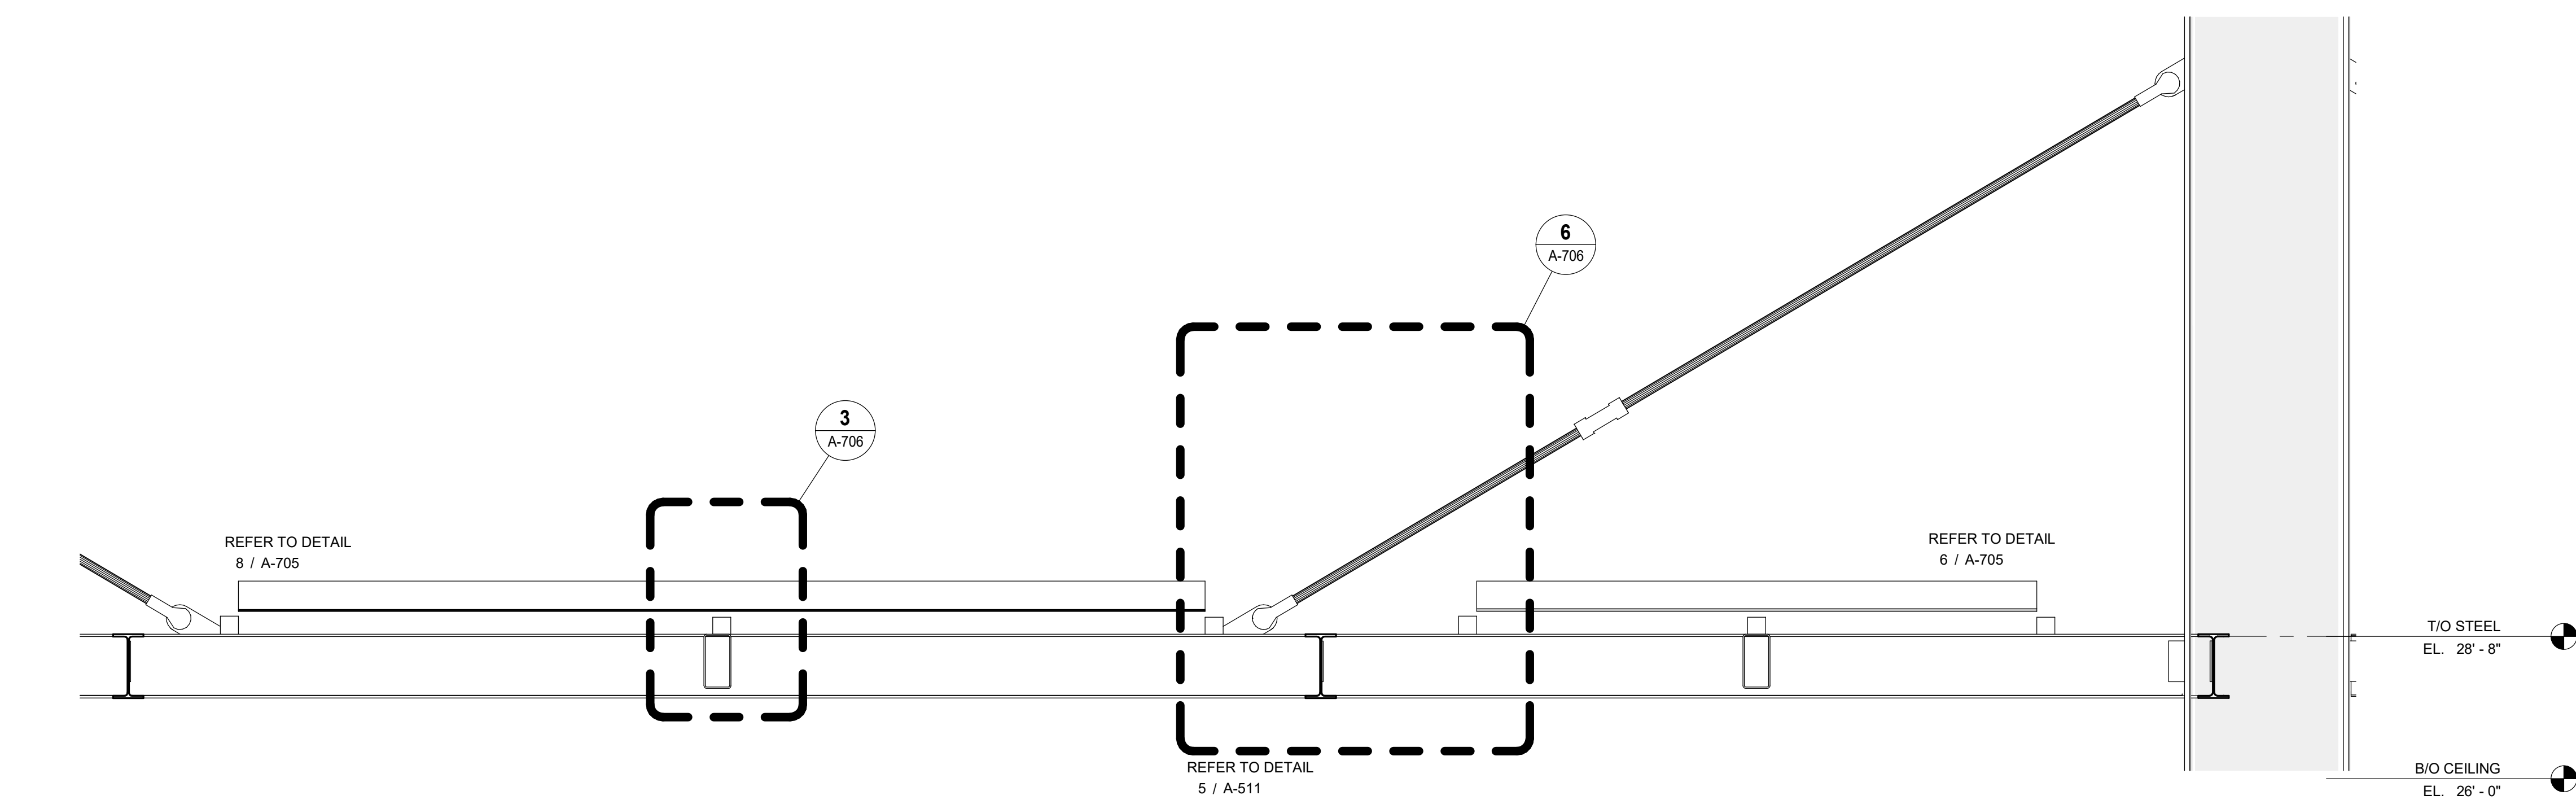

3 SECTION - ENLARGED PARTIAL
SCALE: 1/2" = 1'-0"

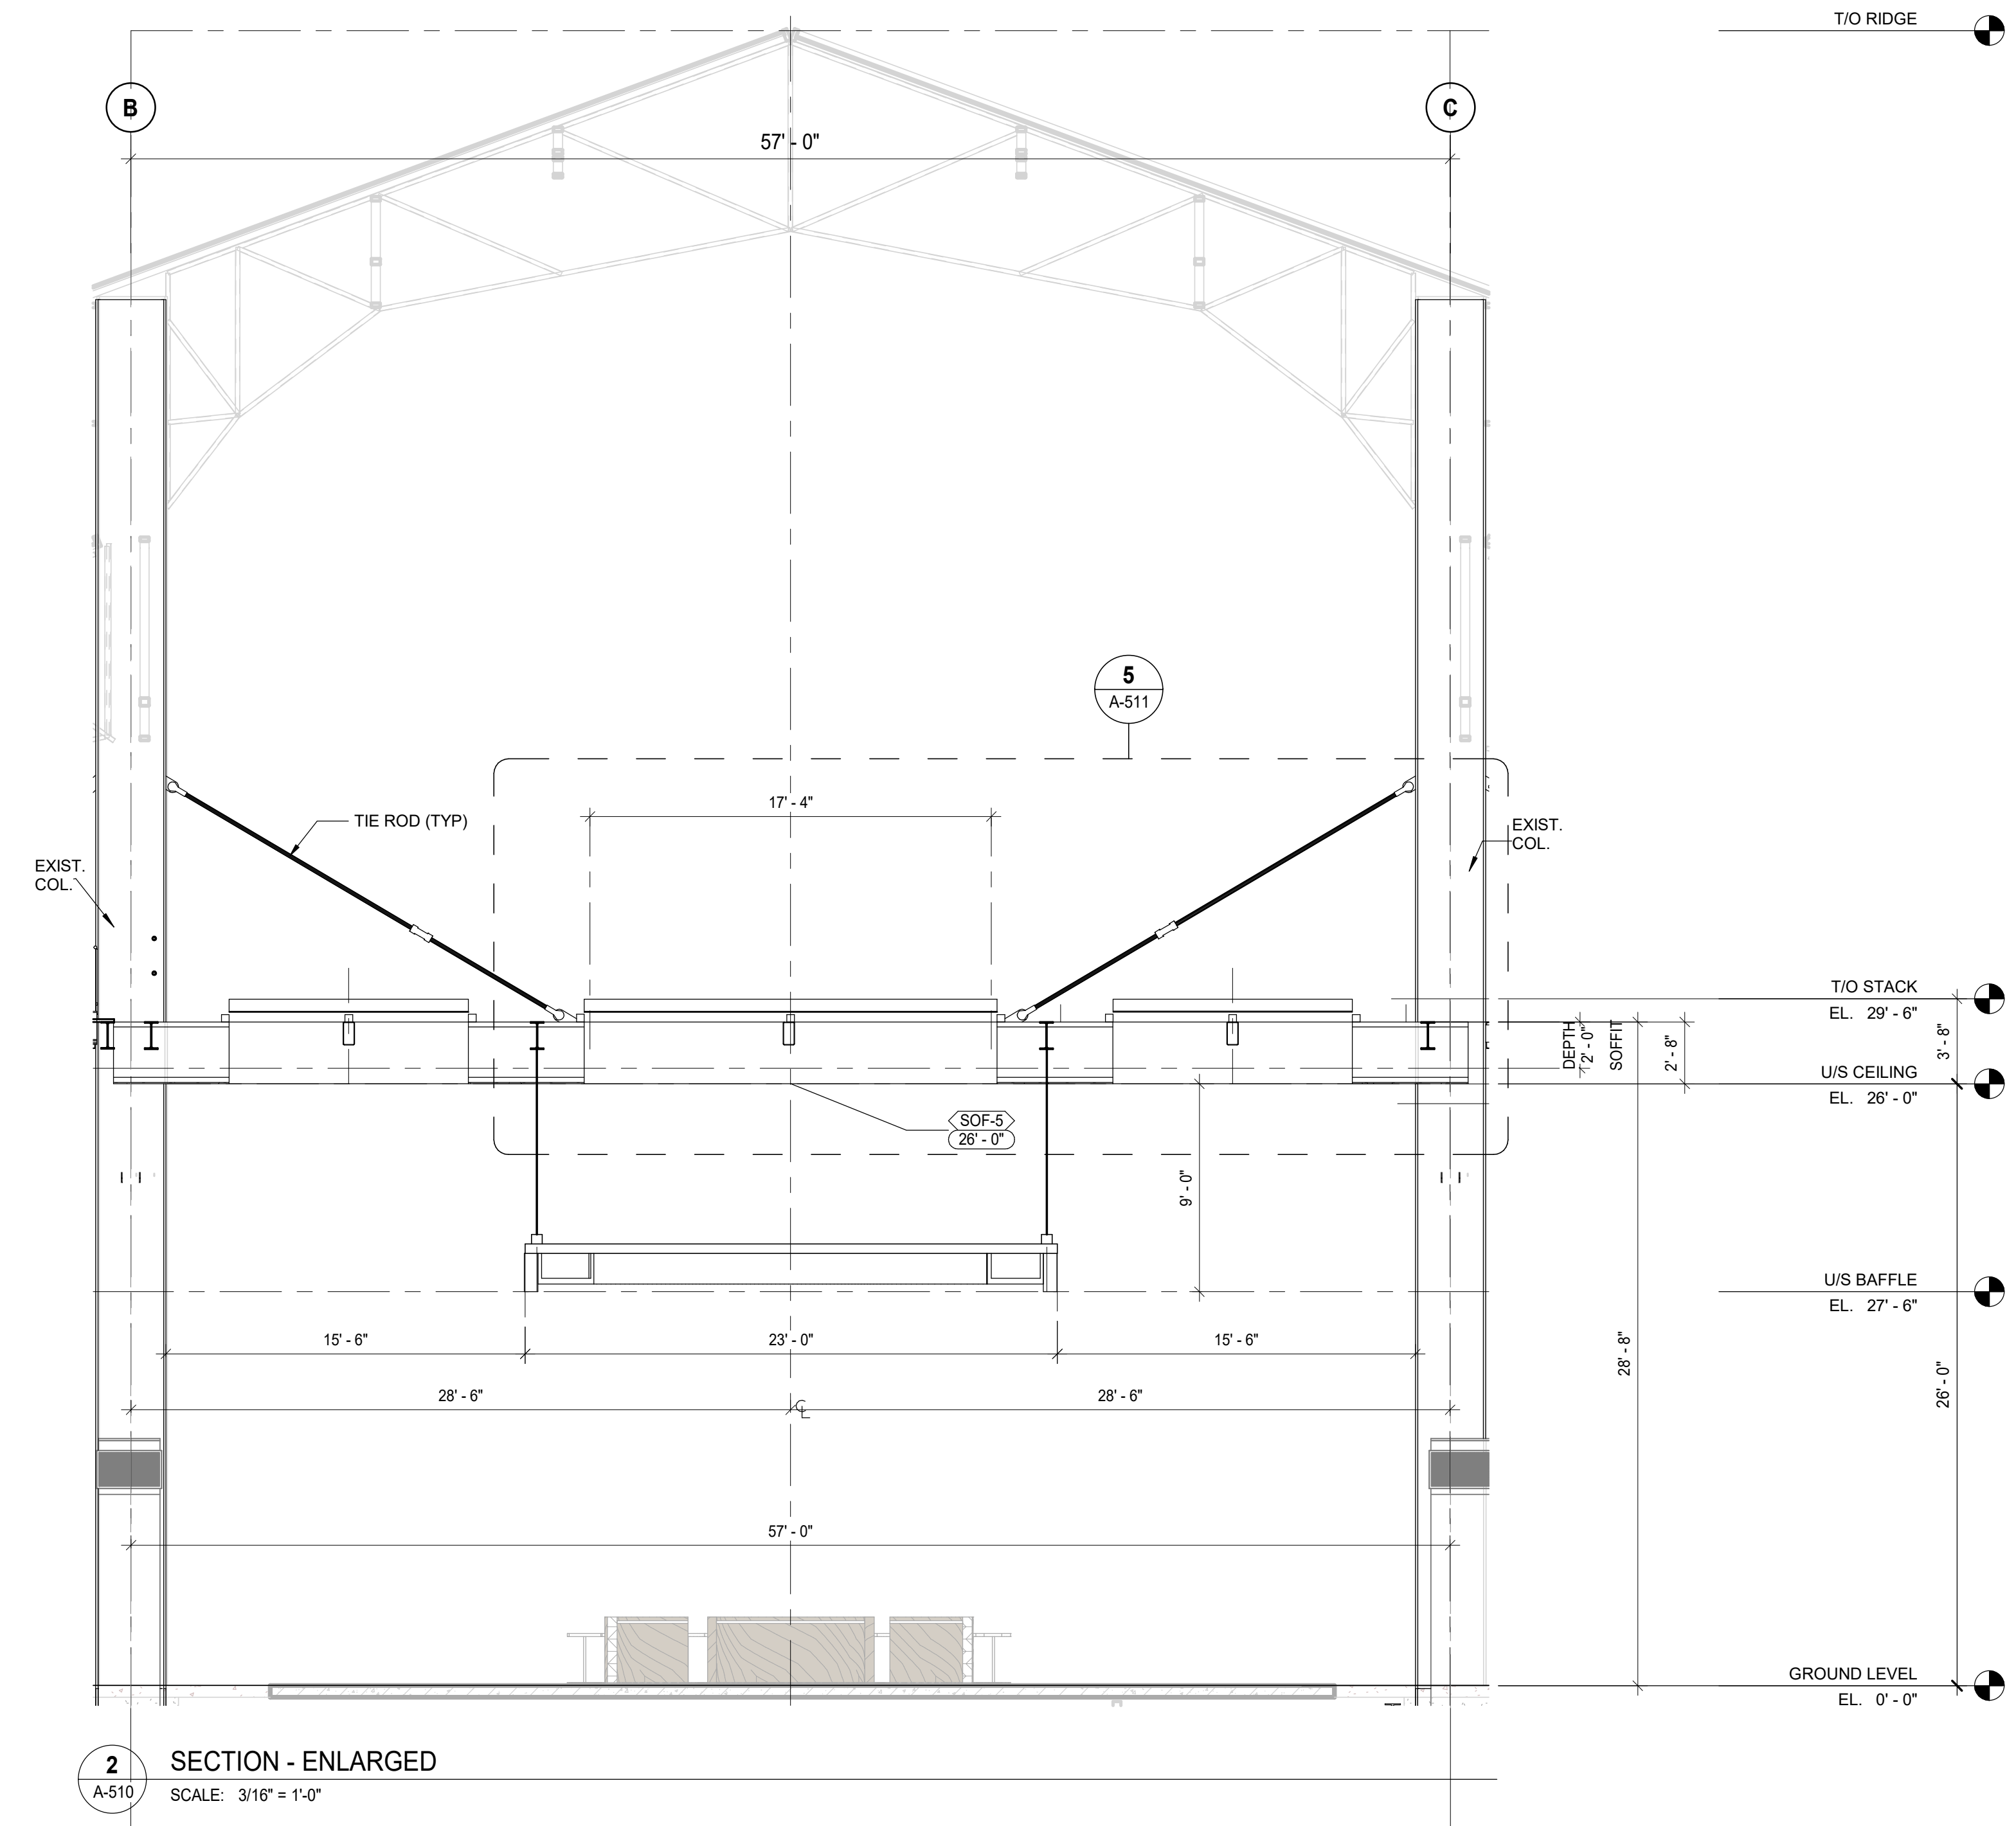

2 SECTION - ENLARGED
SCALE: 3/16" = 1'-0"